

Azuma House · Base · le bâtiment au trait

Feuille 1 · les plans · échelle 1/100 (a = 4 cm) · imprimer à 100 %


Rez-de-chaussée

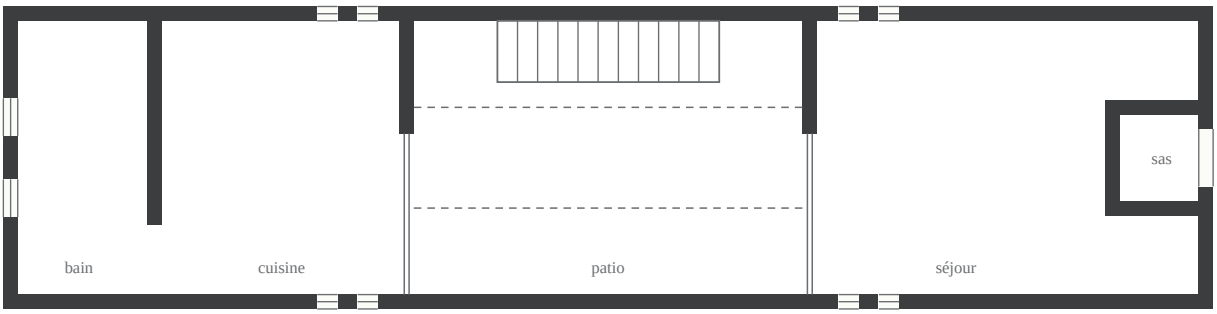

Étage

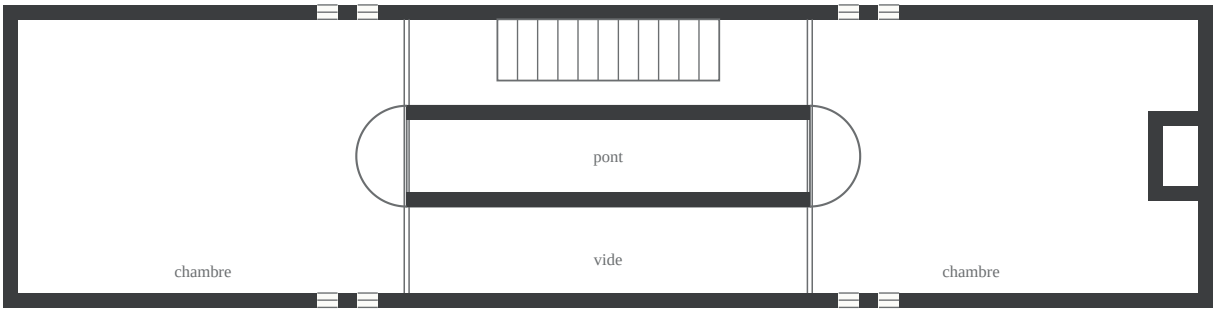

Toiture

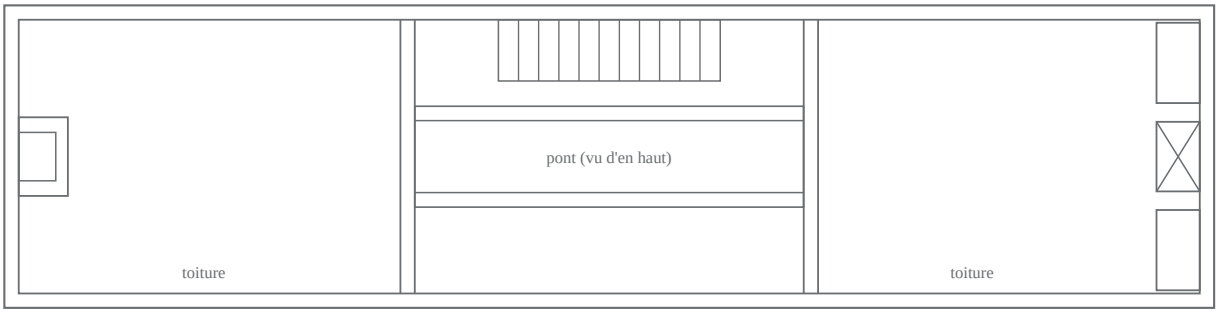


4 cm = a = 4 m

Azuma House · Calque 1 · le carré et le tiers


Feuille 1 · les plans · échelle 1/100 (a = 4 cm) · imprimer à 100 %

a · le carré — **1/3 a · le tiers, 1/15 a** — en gris pâle : repère, à ne pas recopier


Rez-de-chaussée

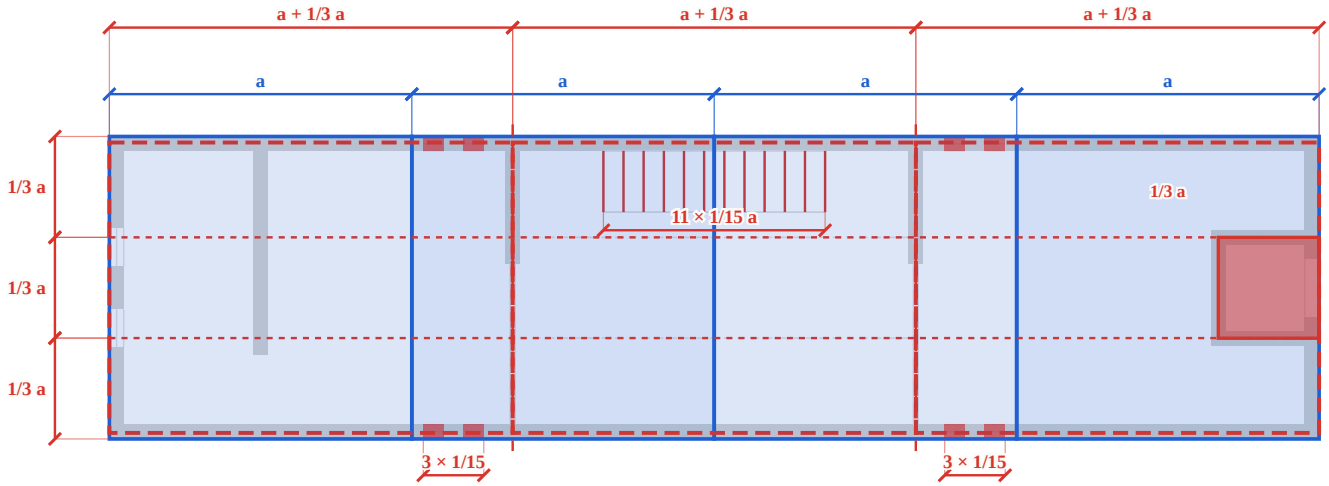

Étage

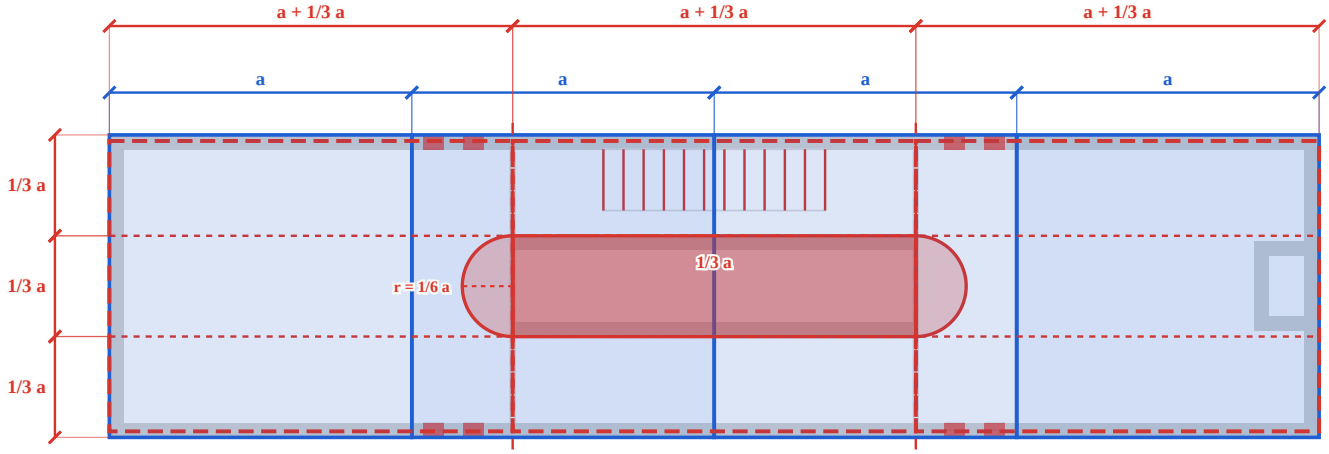

Toiture

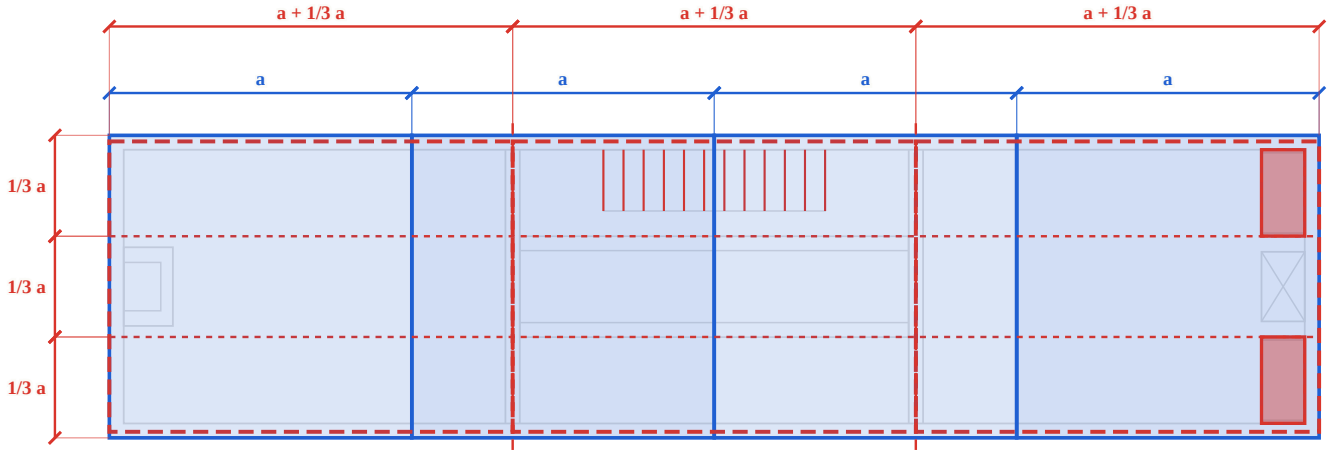


4 cm = a = 4 m

Azuma House · Calque 2 · le quart et le mur


Feuille 1 · les plans · échelle 1/100 (a = 4 cm) · imprimer à 100 %

1/4 a · le quart, 1/8 a **e = 1/21 a · le mur** en gris pâle : repère, à ne pas recopier

Rez-de-chaussée

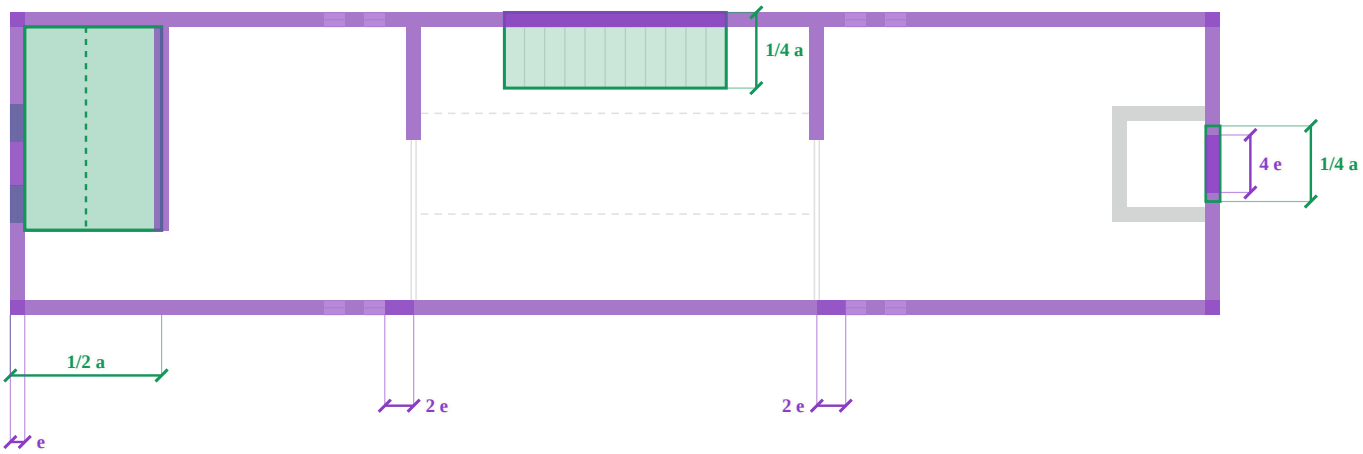

Étage

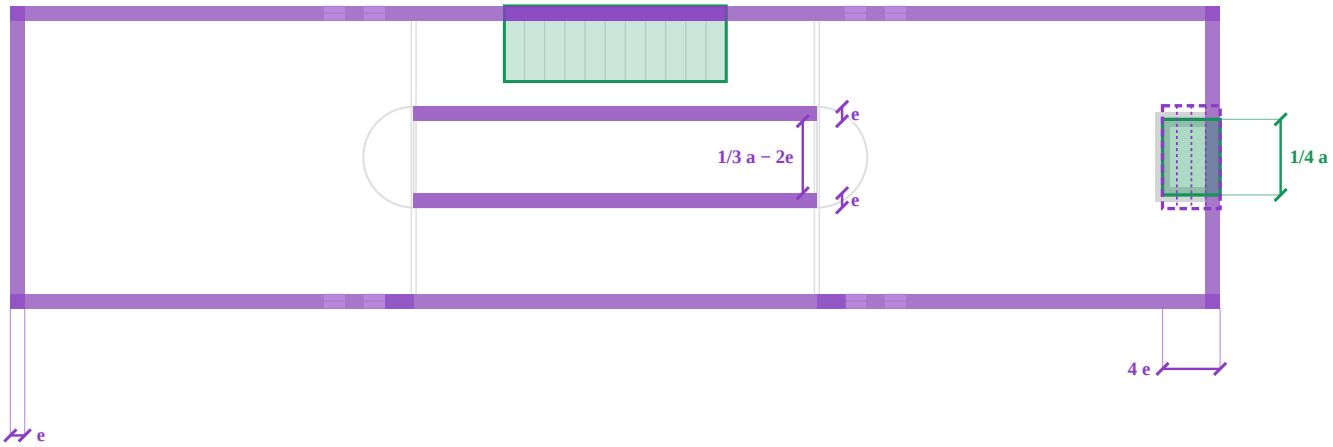

Toiture




4 cm = a = 4 m


Azuma House · Base · le bâtiment au trait

Feuille 2 · coupe longitudinale, coupe C, façade B · échelle 1/100 (a = 4 cm) · imprimer à 100 %


Coupe longitudinale

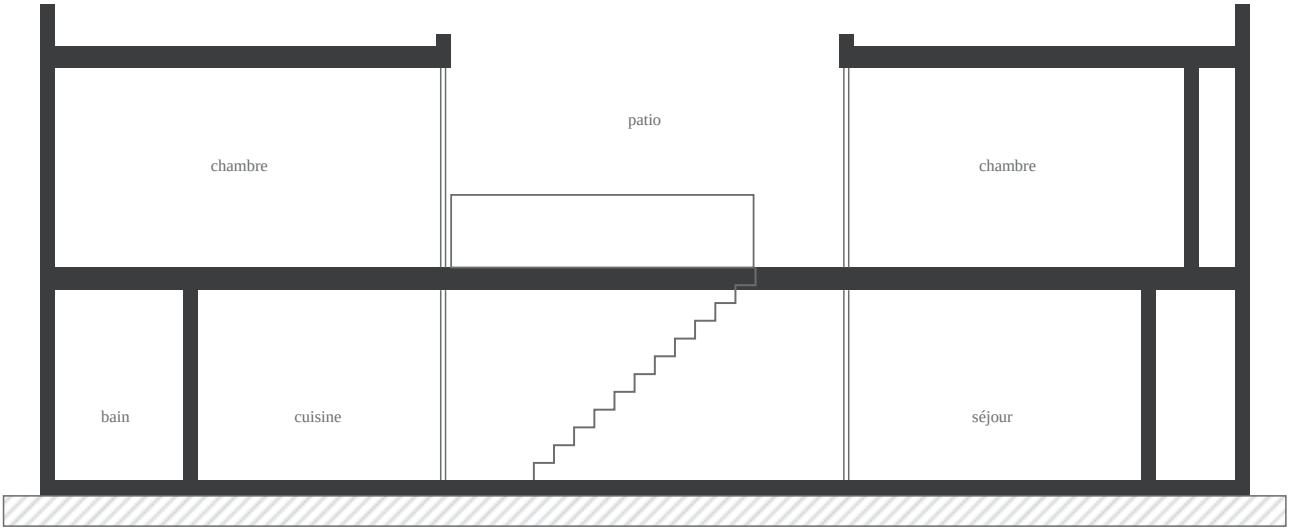

Coupe C

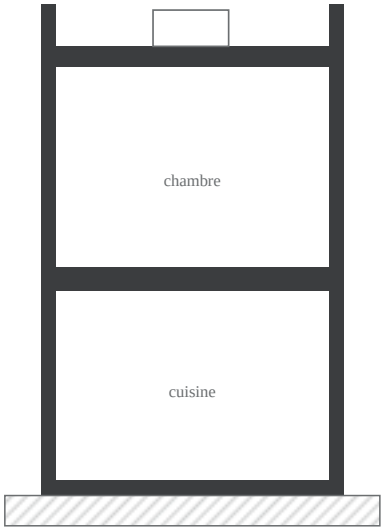

Façade B (rue)

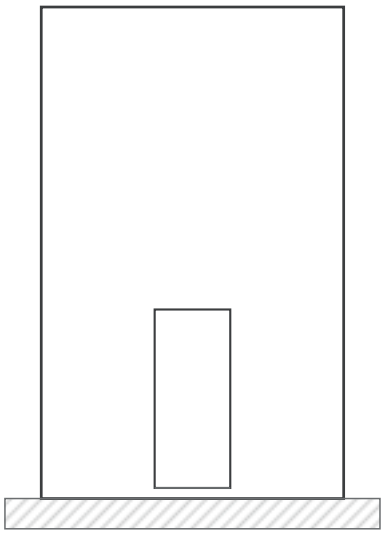


4 cm = a = 4 m

Azuma House · Calque 1 · le carré et le tiers


Feuille 2 · coupe longitudinale, coupe C, façade B · échelle 1/100 (a = 4 cm) · imprimer à 100 %

a · le carré **1/3 a · le tiers, 1/15 a** en gris pâle : repère, à ne pas recopier


Coupe longitudinale

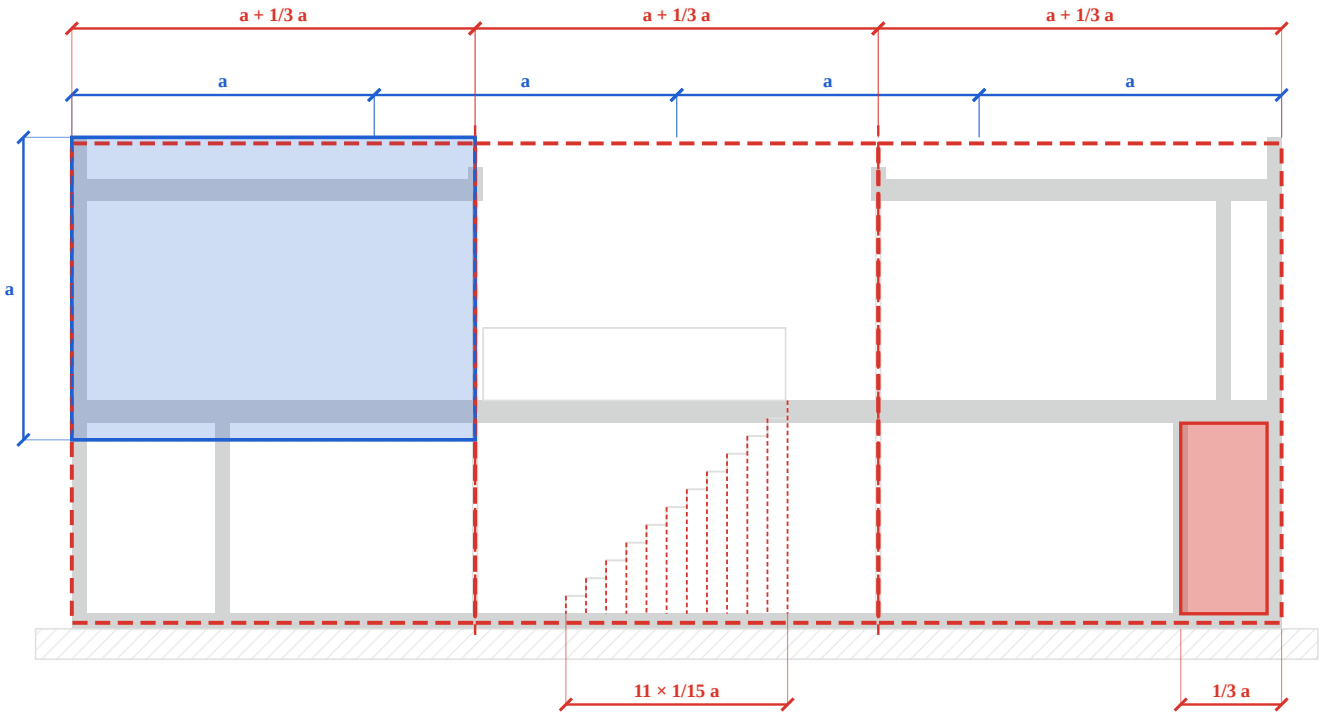

Coupe C

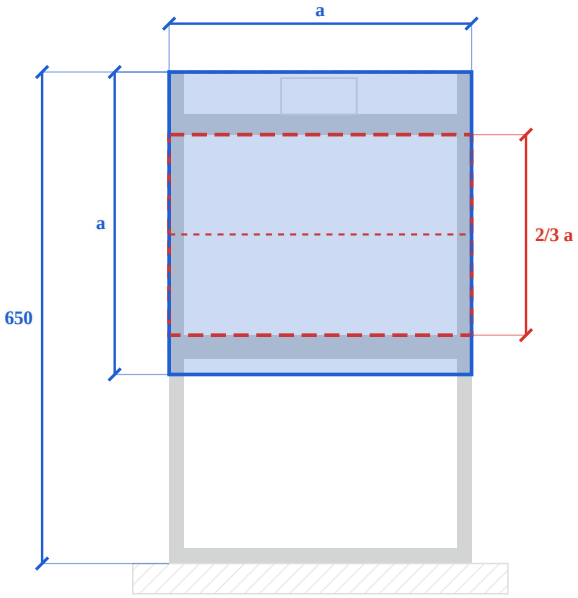

Façade B (rue)

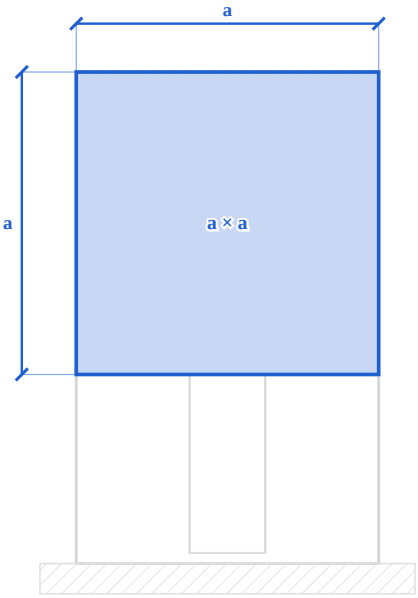


4 cm = a = 4 m

Azuma House · Calque 2 · le quart et le mur


Feuille 2 · coupe longitudinale, coupe C, façade B · échelle 1/100 (a = 4 cm) · imprimer à 100 %

1/4 a · le quart, 1/8 a **e = 1/21 a · le mur** en gris pâle : repère, à ne pas recopier


Coupe longitudinale

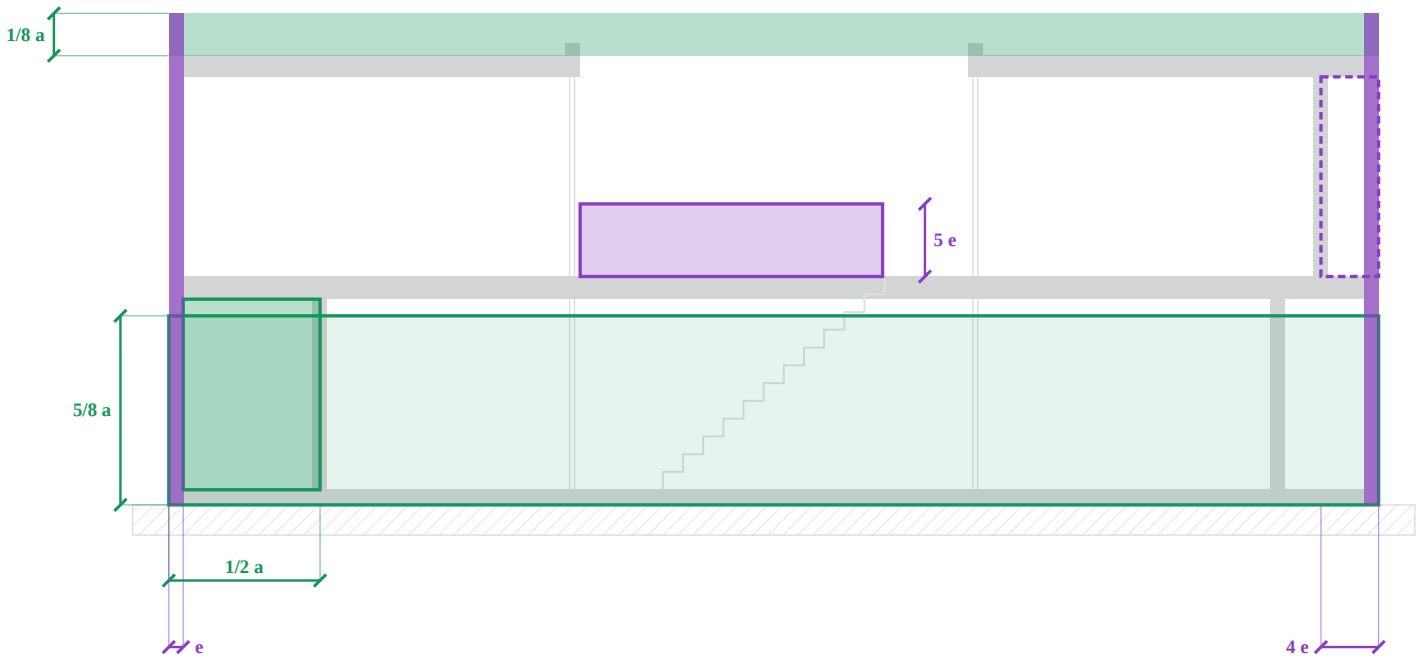

Coupe C

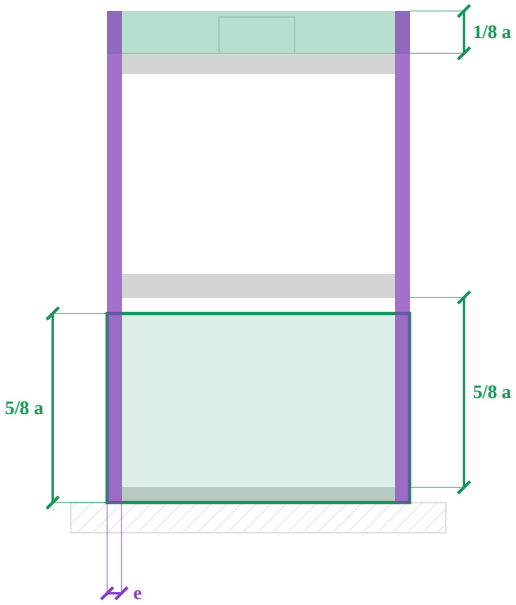

Façade B (rue)

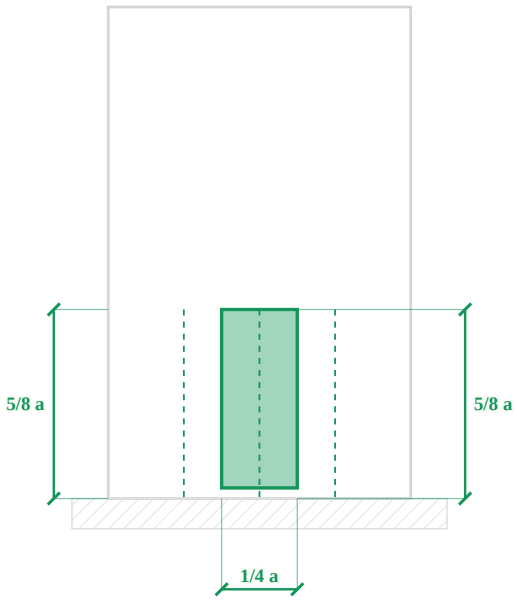


4 cm = a = 4 m


Azuma House · Base · le bâtiment au trait

Feuille 3 · coupe E, façade C · échelle 1/100 (a = 4 cm) · imprimer à 100 %

Coupe E (patio)

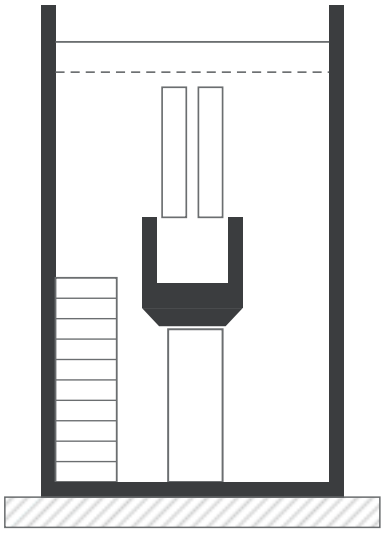

Façade C (jardin)

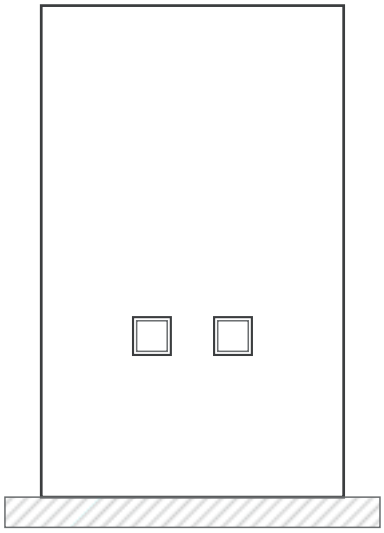


4 cm = a = 4 m

Azuma House · Calque 1 · le carré et le tiers


Feuille 3 · coupe E, façade C · échelle 1/100 (a = 4 cm) · imprimer à 100 %

a · le carré **1/3 a · le tiers, 1/15 a** en gris pâle : repère, à ne pas recopier

Coupe E (patio)

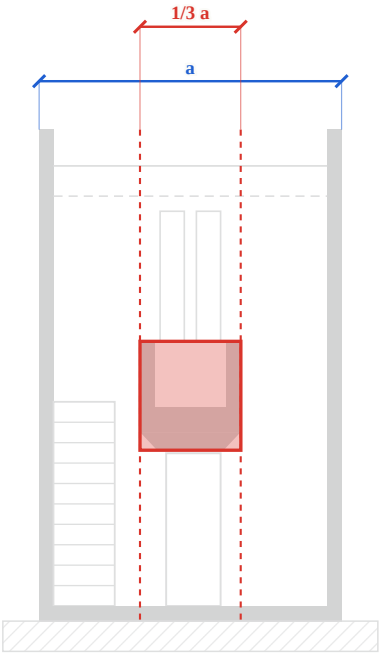

Façade C (jardin)

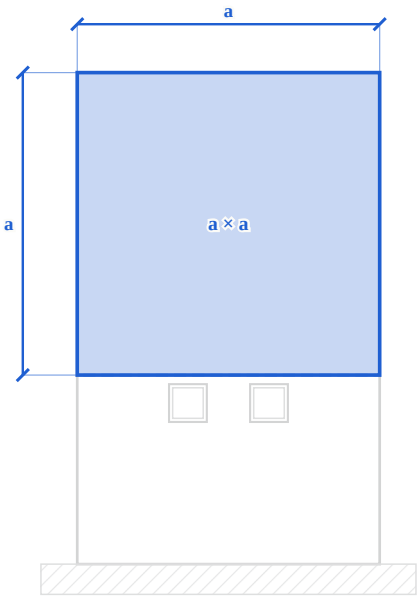


4 cm = a = 4 m

Azuma House · Calque 2 · le quart et le mur


Feuille 3 · coupe E, façade C · échelle 1/100 (a = 4 cm) · imprimer à 100 %

1/4 a · le quart, 1/8 a **e = 1/21 a · le mur** en gris pâle : repère, à ne pas recopier

Coupe E (patio)

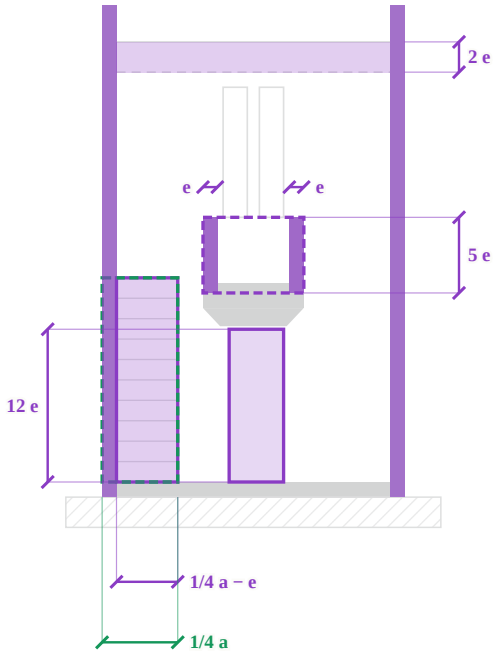

Façade C (jardin)

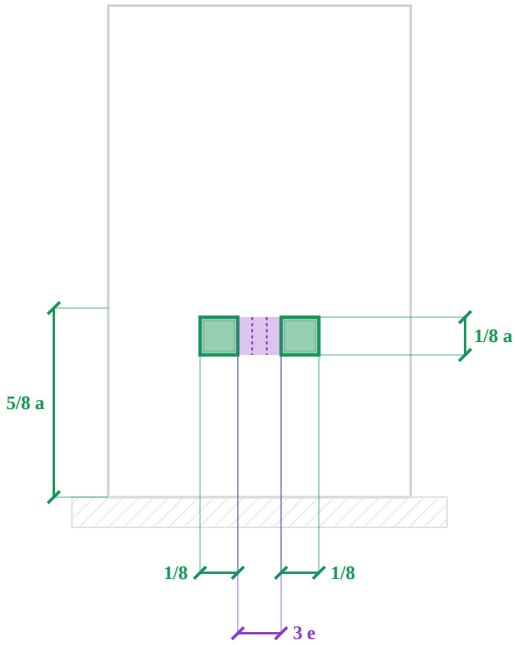


4 cm = a = 4 m

Azuma House · La trame · modules de 1/3 a


Feuille 4 · la trame · échelle 1/100 (a = 4 cm) · imprimer à 100 %

a = 3 modules **1/3 a = 1 module**


Rez-de-chaussée sur la trame

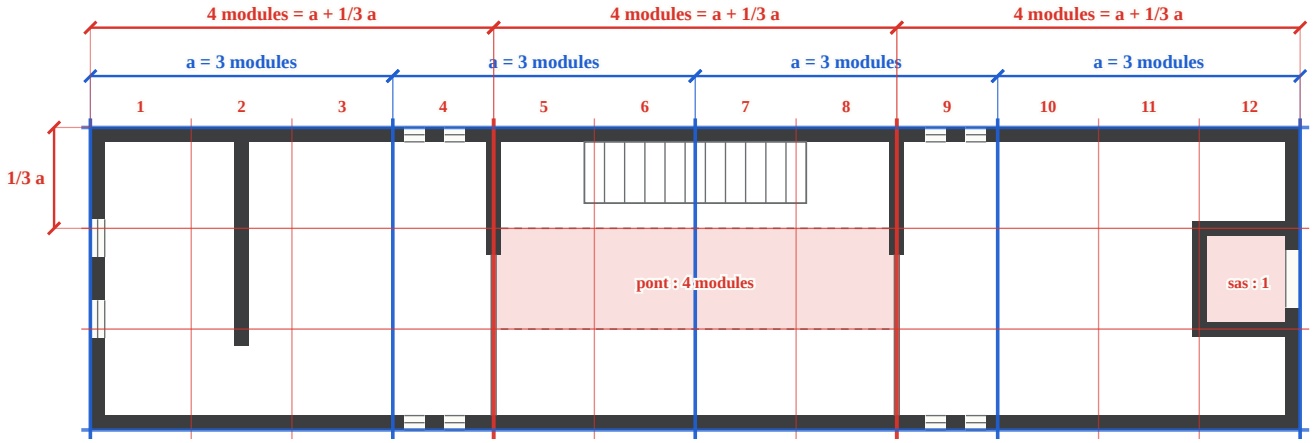

Étage sur la trame

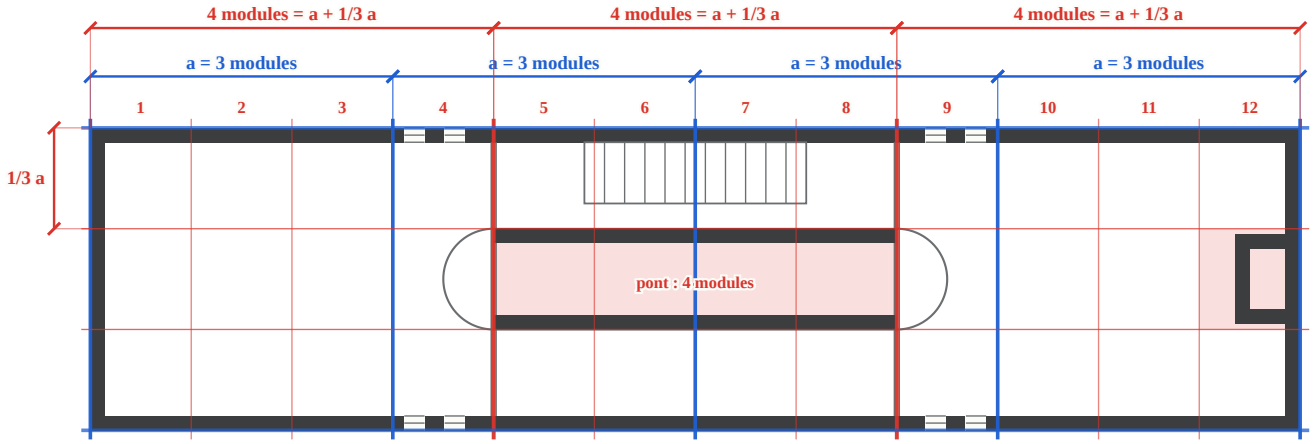

Toiture sur la trame

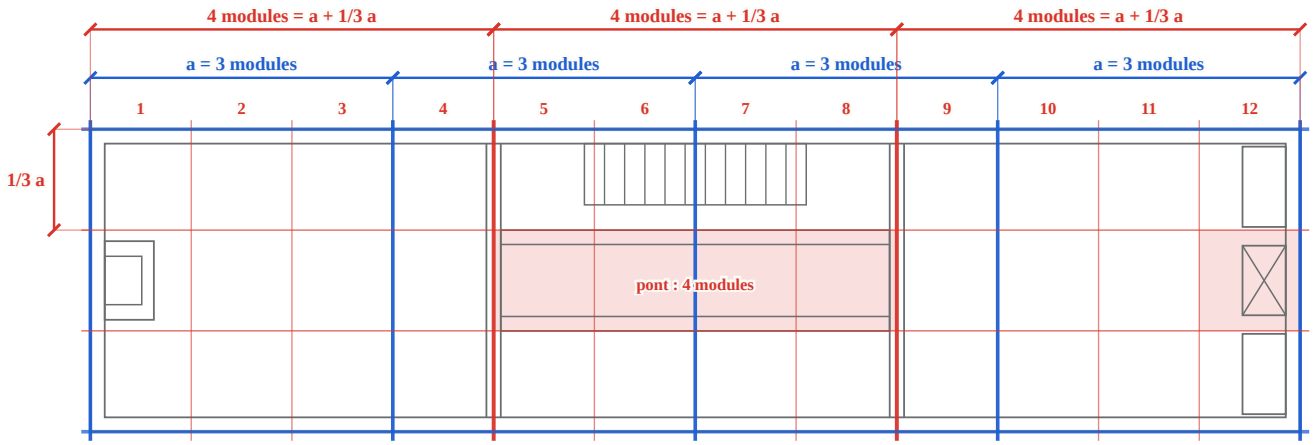

4 cm = a = 4 m