

Azuma House · Base · le bâtiment au trait

Feuille 1 · les plans · échelle 1/100 (a = 4 cm) · imprimer à 100 %


Rez-de-chaussée

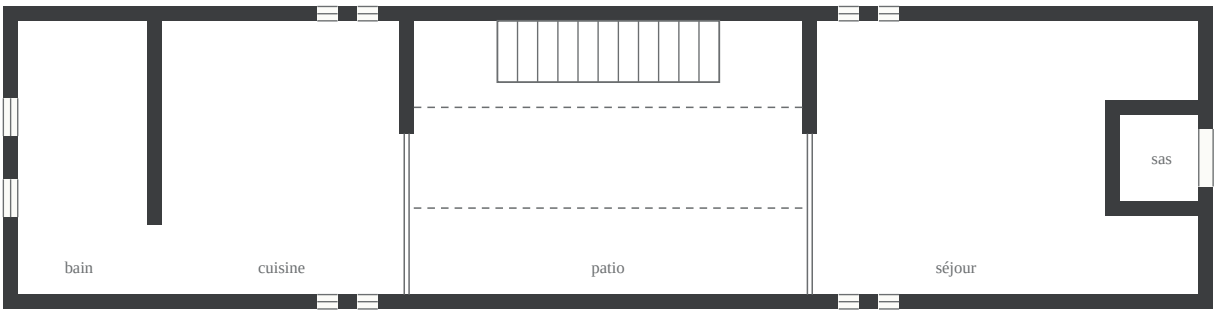

Étage

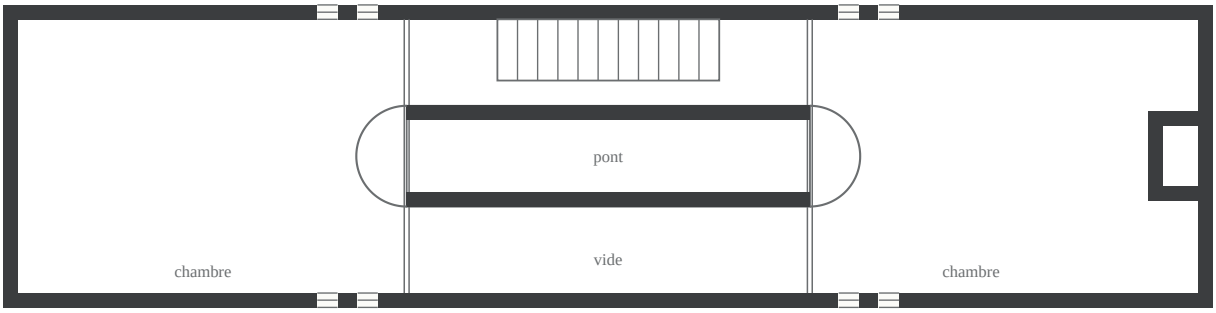

Toiture

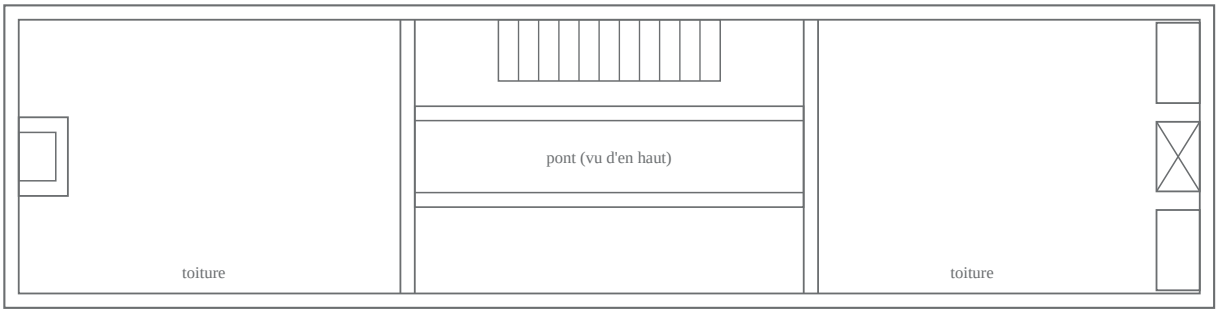


4 cm = a = 4 m

Azuma House · Calque 1 · le carré et le tiers


Feuille 1 · les plans · échelle 1/100 (a = 4 cm) · imprimer à 100 %

a · le carré — **1/3 a · le tiers, 1/15 a** — en gris pâle : repère, à ne pas recopier


Rez-de-chaussée

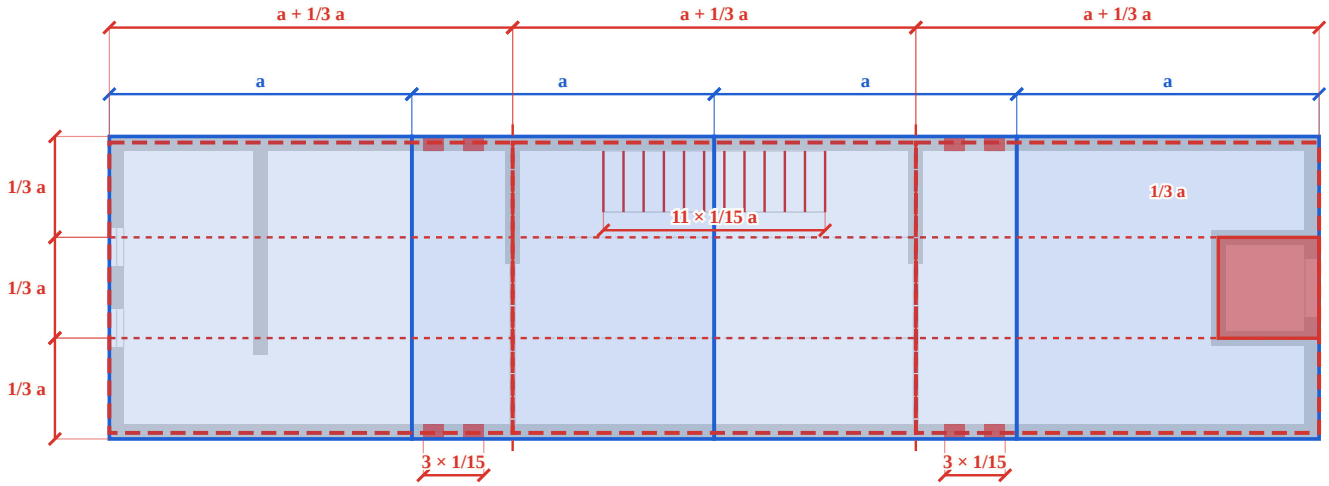

Étage

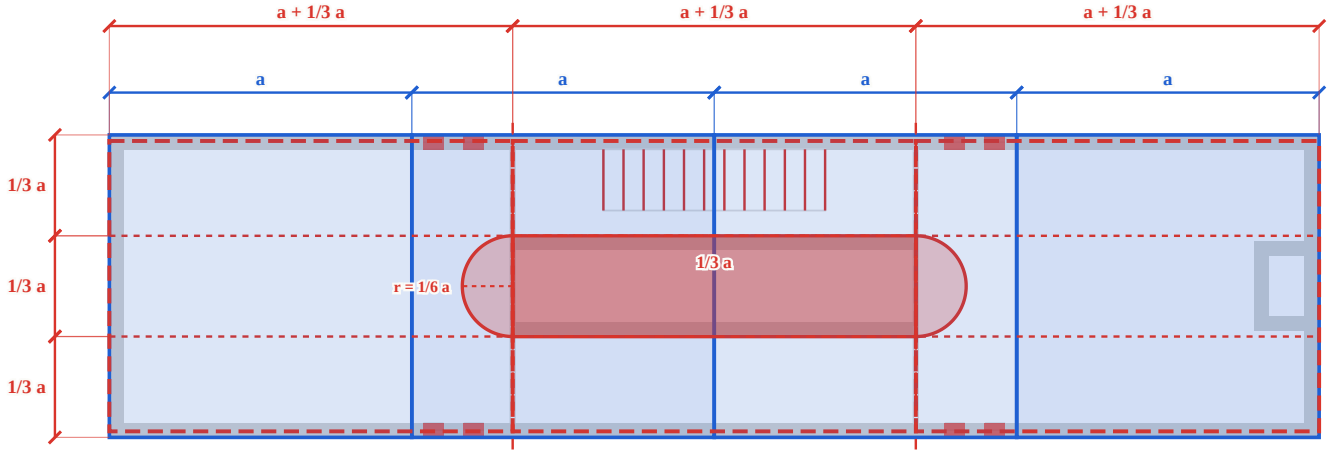

Toiture

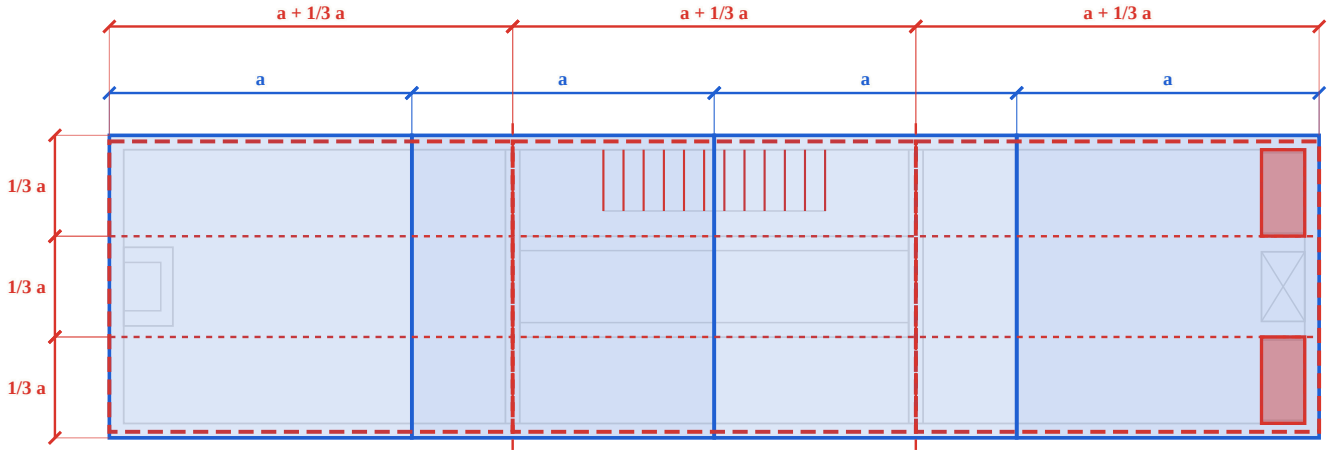


4 cm = a = 4 m

Azuma House · Calque 2 · le quart et le mur


Feuille 1 · les plans · échelle 1/100 (a = 4 cm) · imprimer à 100 %

1/4 a · le quart, 1/8 a **e = 1/21 a · le mur** en gris pâle : repère, à ne pas recopier

Rez-de-chaussée

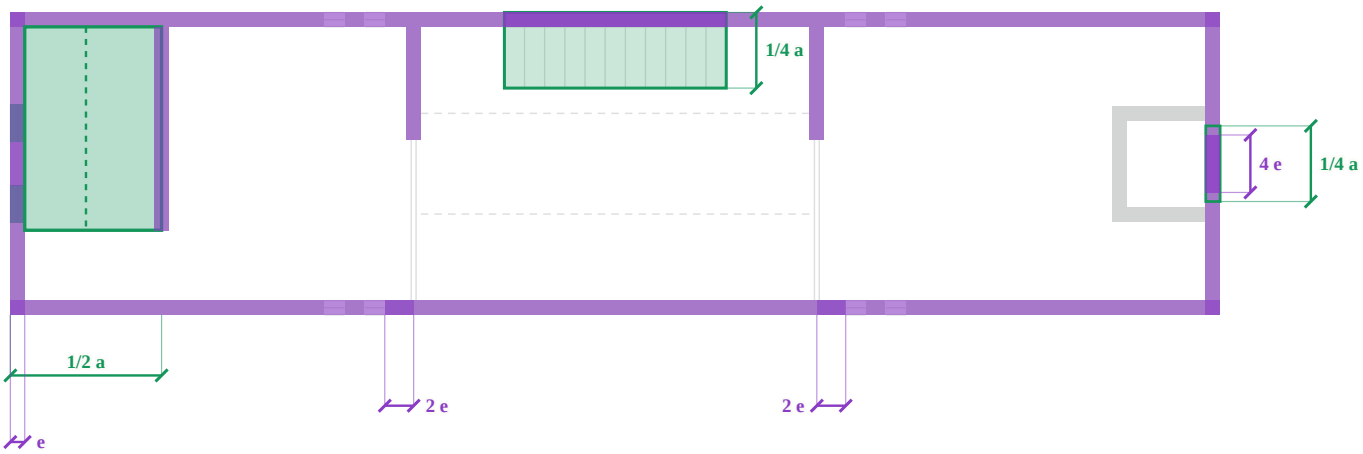

Étage

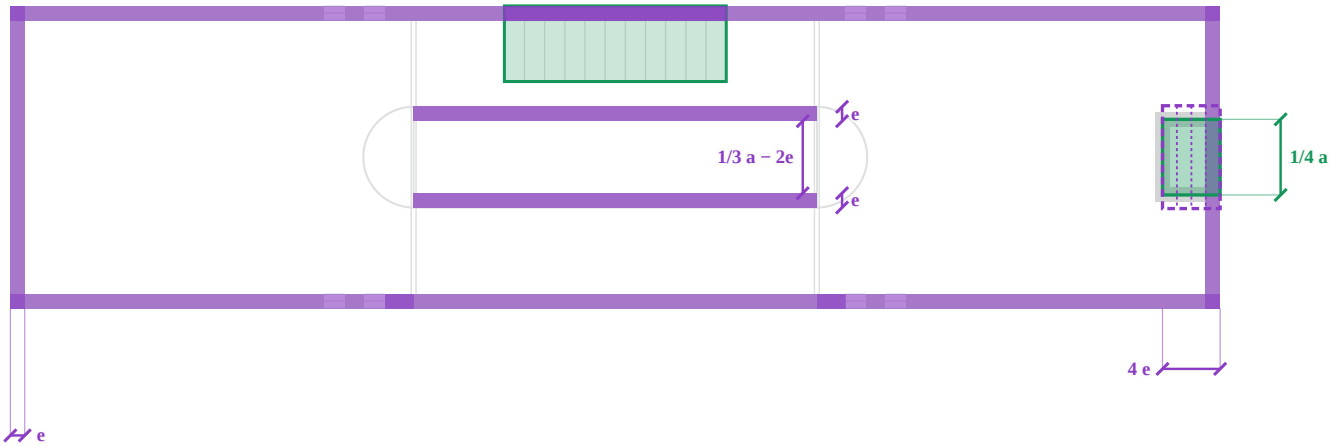

Toiture




4 cm = a = 4 m


Azuma House · Base · le bâtiment au trait

Feuille 2 · coupe longitudinale, coupe C, façade B · échelle 1/100 (a = 4 cm) · imprimer à 100 %


Coupe longitudinale

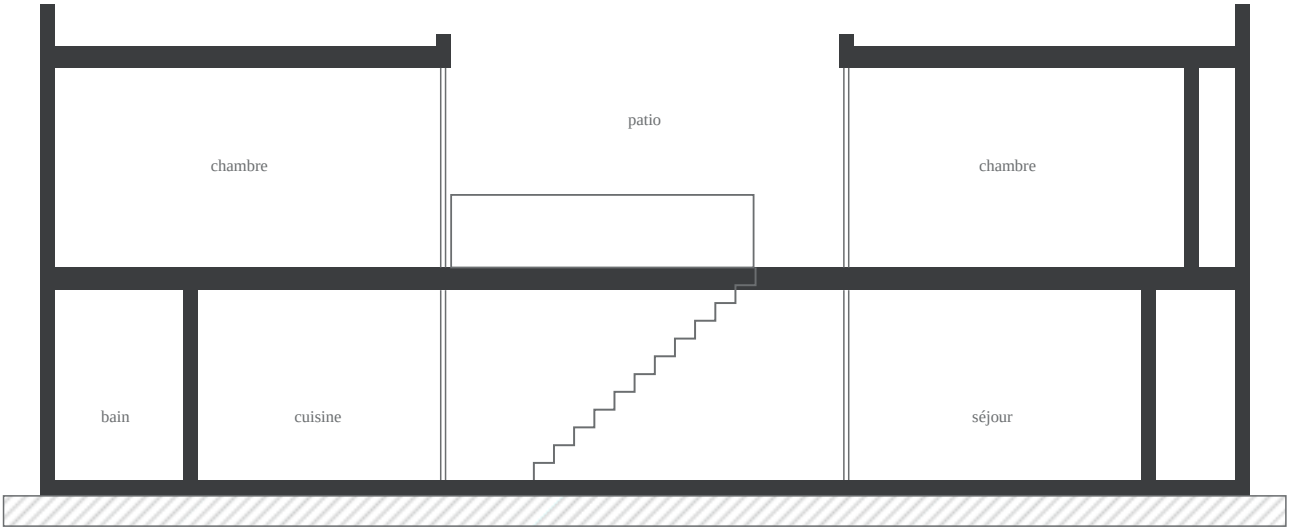

Coupe C

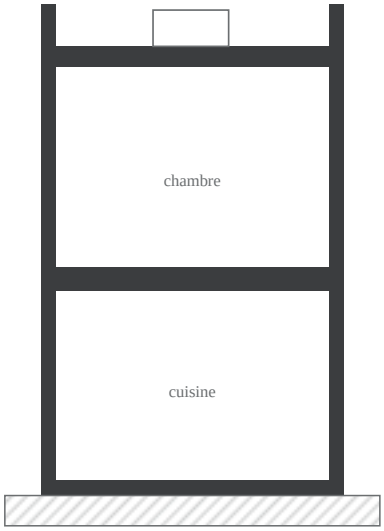

Façade B (rue)

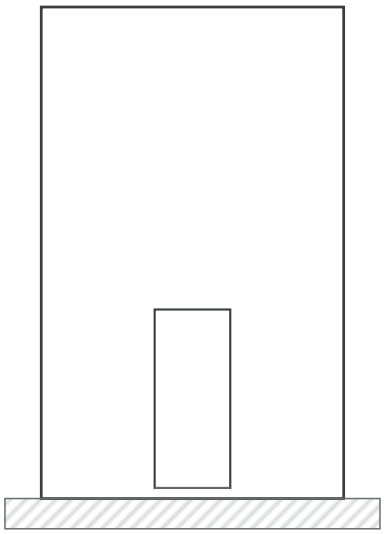


4 cm = a = 4 m

Azuma House · Calque 1 · le carré et le tiers


Feuille 2 · coupe longitudinale, coupe C, façade B · échelle 1/100 (a = 4 cm) · imprimer à 100 %

a · le carré **1/3 a · le tiers, 1/15 a** en gris pâle : repère, à ne pas recopier


Coupe longitudinale

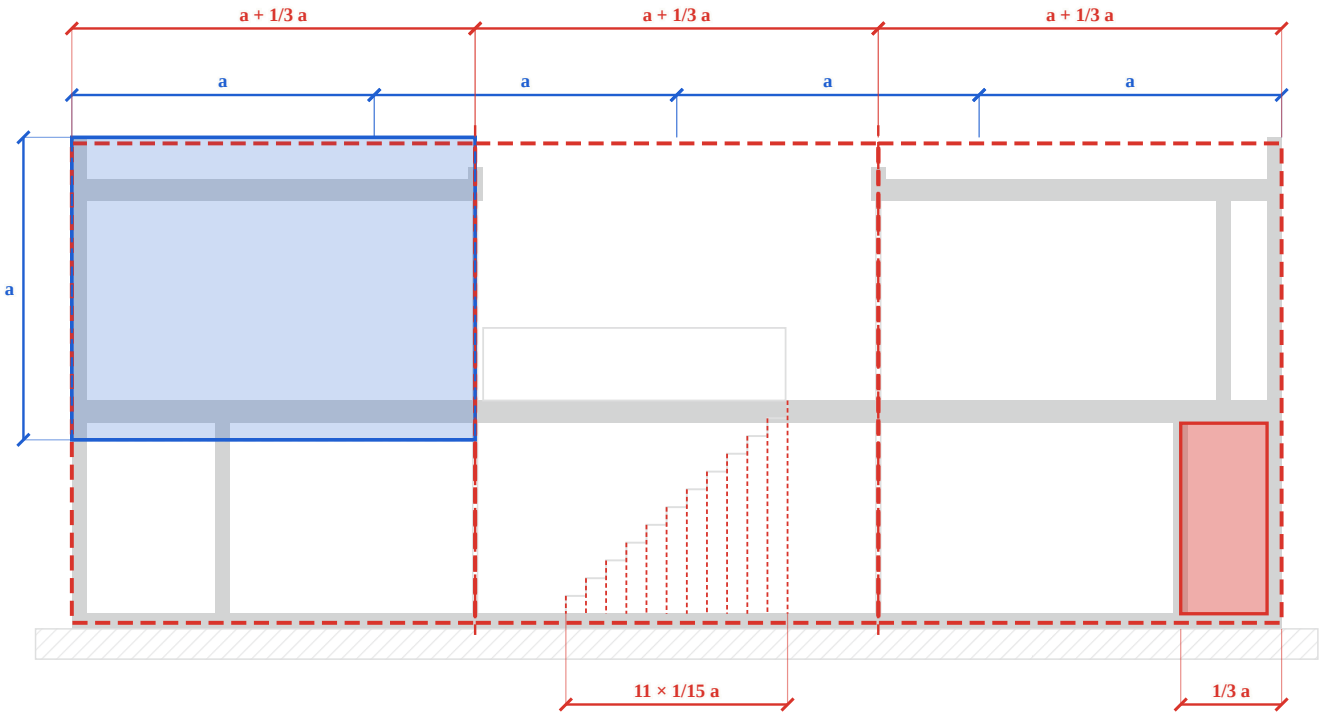

Coupe C

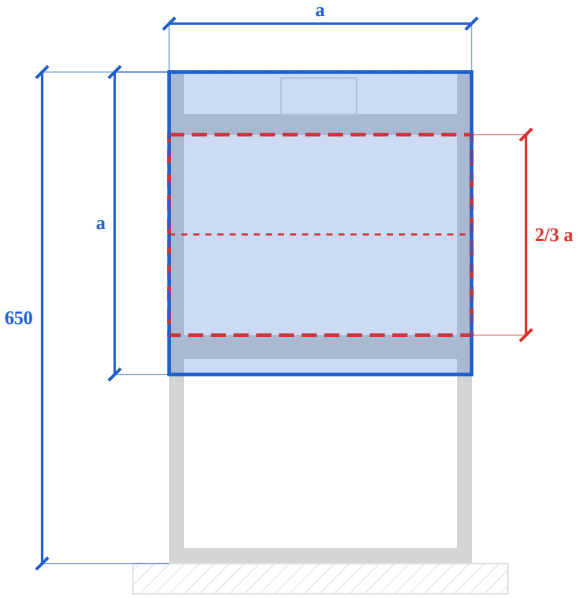

Façade B (rue)

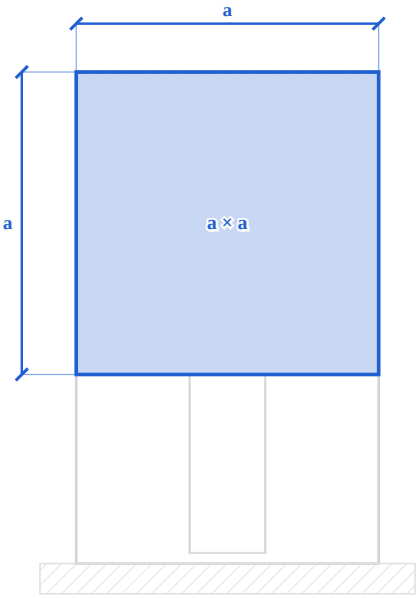


4 cm = a = 4 m

Azuma House · Calque 2 · le quart et le mur


Feuille 2 · coupe longitudinale, coupe C, façade B · échelle 1/100 (a = 4 cm) · imprimer à 100 %

1/4 a · le quart, 1/8 a **e = 1/21 a · le mur** en gris pâle : repère, à ne pas recopier


Coupe longitudinale

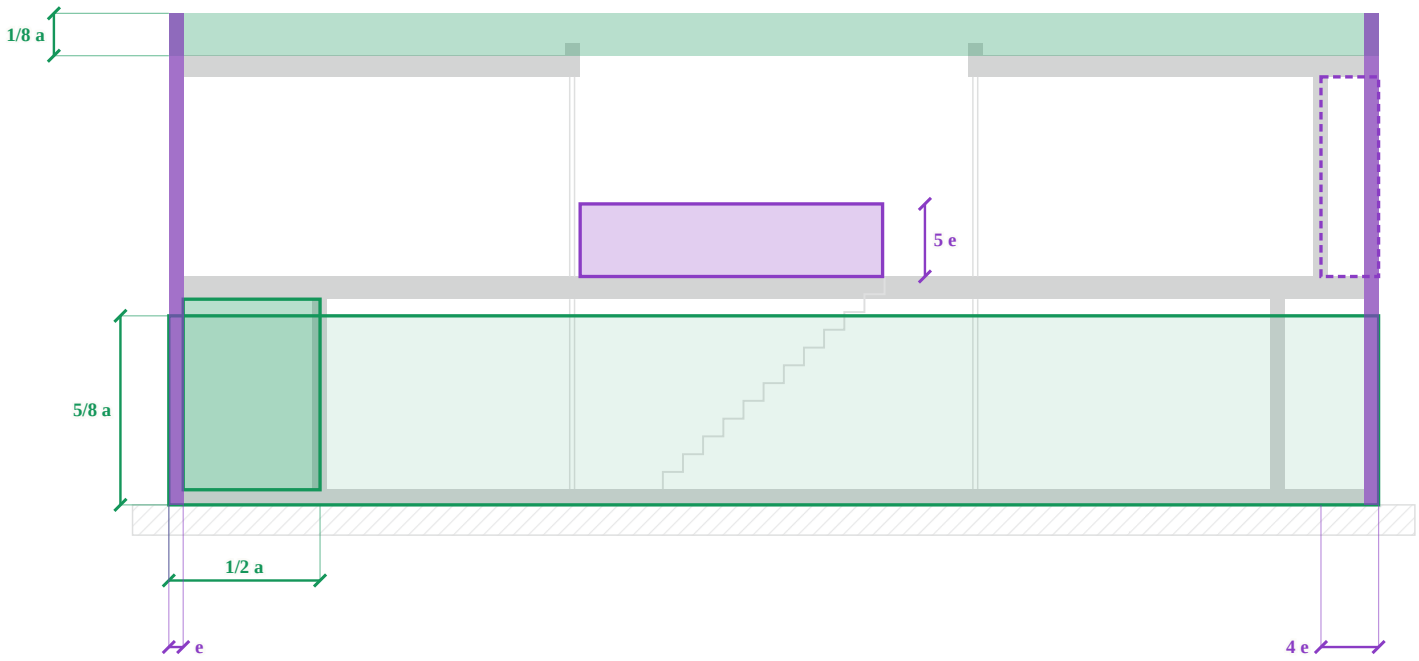

Coupe C

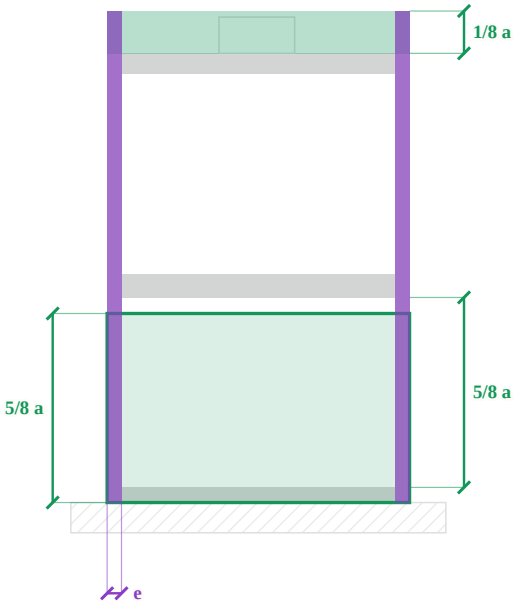

Façade B (rue)

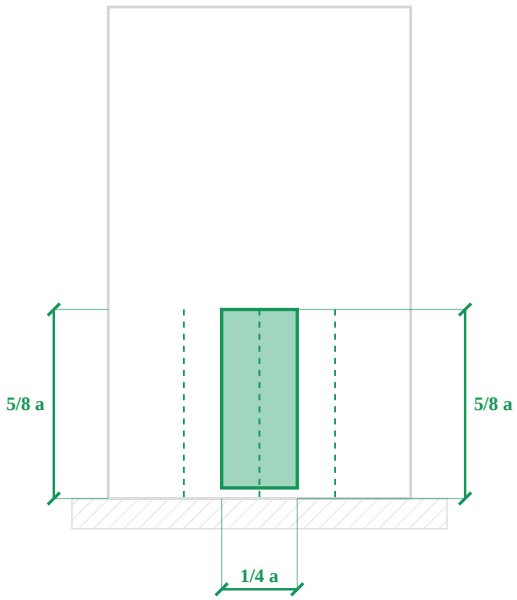


4 cm = a = 4 m


Azuma House · Base · le bâtiment au trait

Feuille 3 · coupe E, façade C · échelle 1/100 (a = 4 cm) · imprimer à 100 %

Coupe E (patio)

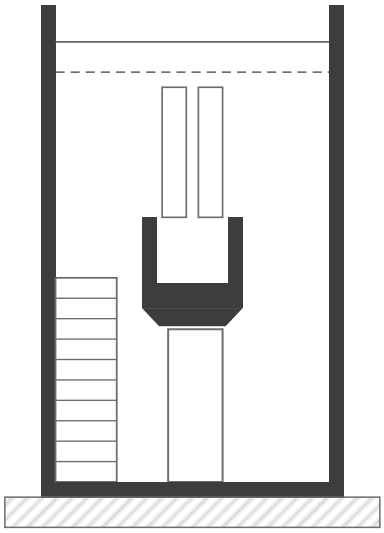

Façade C (jardin)

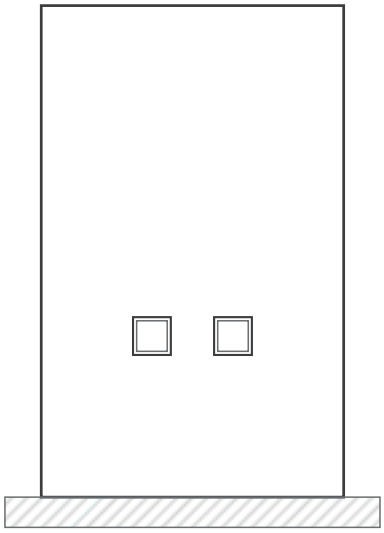


4 cm = a = 4 m

Azuma House · Calque 1 · le carré et le tiers


Feuille 3 · coupe E, façade C · échelle 1/100 (a = 4 cm) · imprimer à 100 %

a · le carré **1/3 a · le tiers, 1/15 a** en gris pâle : repère, à ne pas recopier

Coupe E (patio)

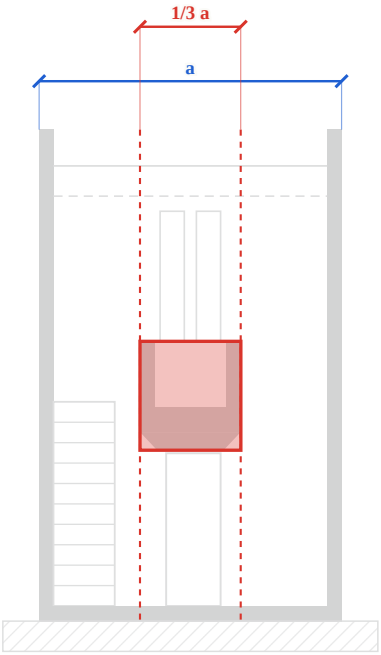

Façade C (jardin)

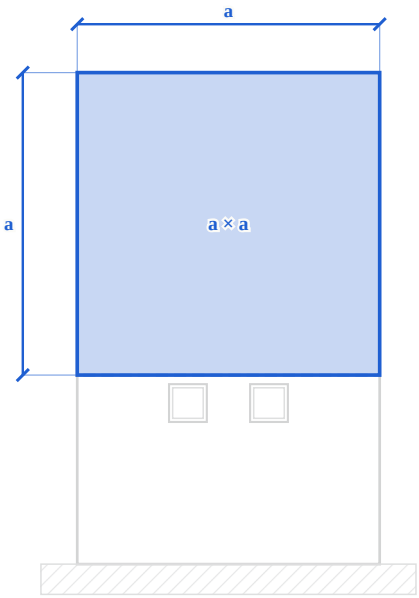


4 cm = a = 4 m

Azuma House · Calque 2 · le quart et le mur


Feuille 3 · coupe E, façade C · échelle 1/100 (a = 4 cm) · imprimer à 100 %

1/4 a · le quart, 1/8 a **e = 1/21 a · le mur** en gris pâle : repère, à ne pas recopier

Coupe E (patio)

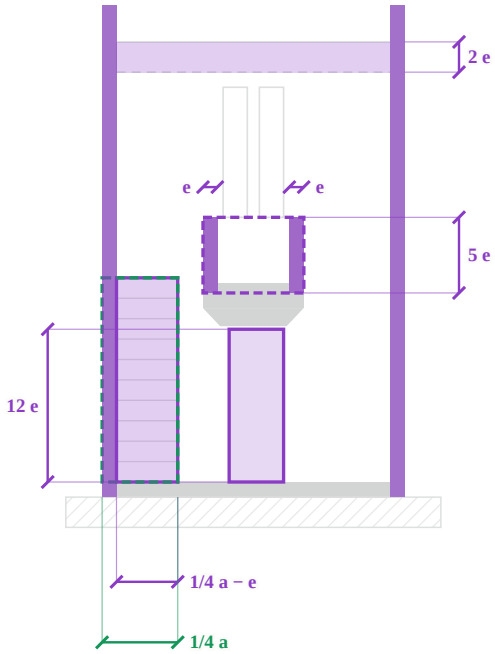

Façade C (jardin)

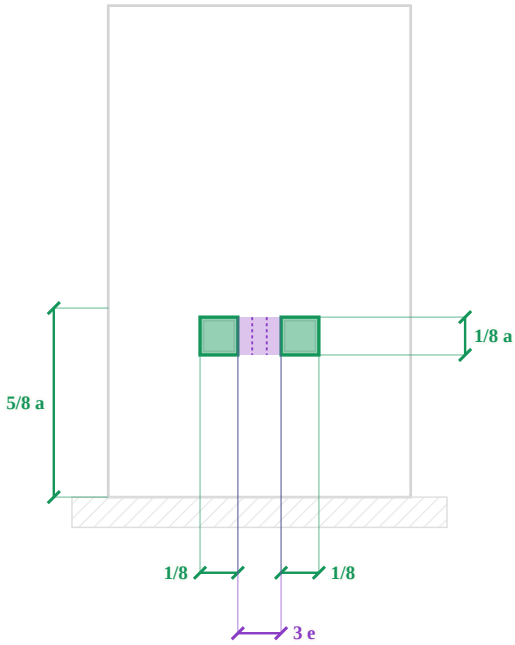


4 cm = a = 4 m

Azuma House · La trame · modules de 1/3 a


Feuille 4 · la trame · échelle 1/100 (a = 4 cm) · imprimer à 100 %

a = 3 modules **1/3 a = 1 module**


Rez-de-chaussée sur la trame

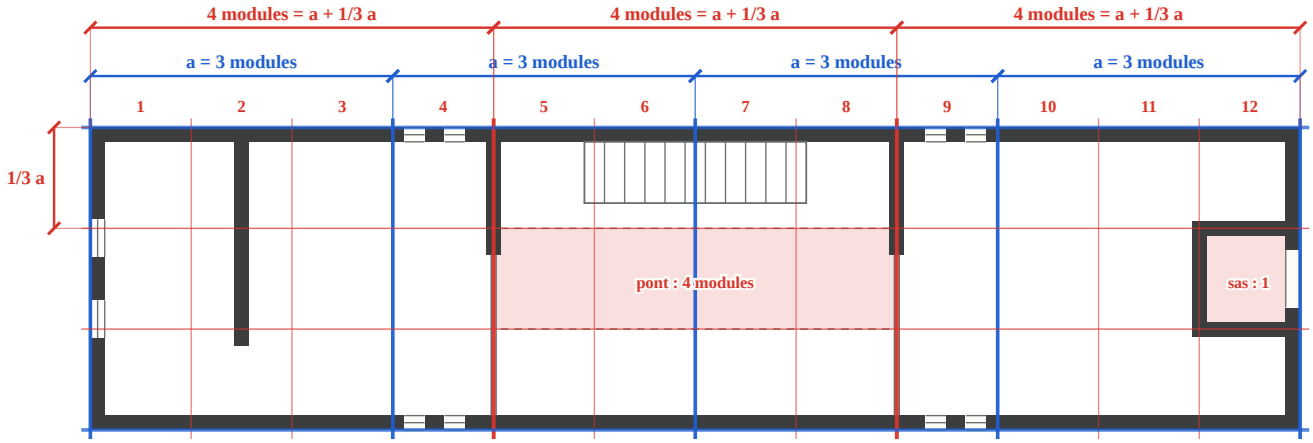

Étage sur la trame

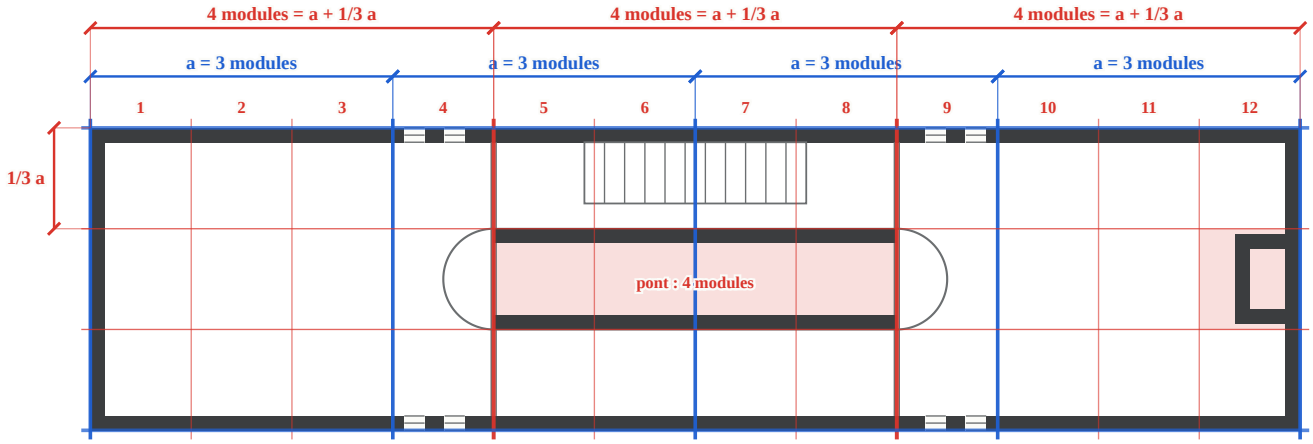

Toiture sur la trame

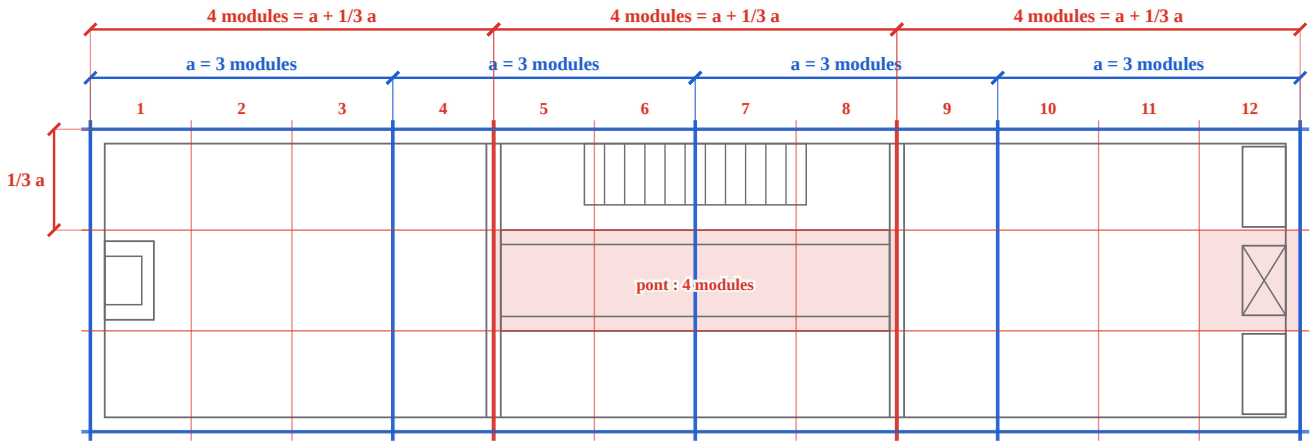


4 cm = a = 4 m

Azuma House · Les plis, étape par étape


Feuille 5 · les plis (1/3) · échelle 1/100 (a = 4 cm) · imprimer à 100 %

plis du carré · plis du tiers · plis du quart · plis du mur


Pli 1 · le plan plié en 2

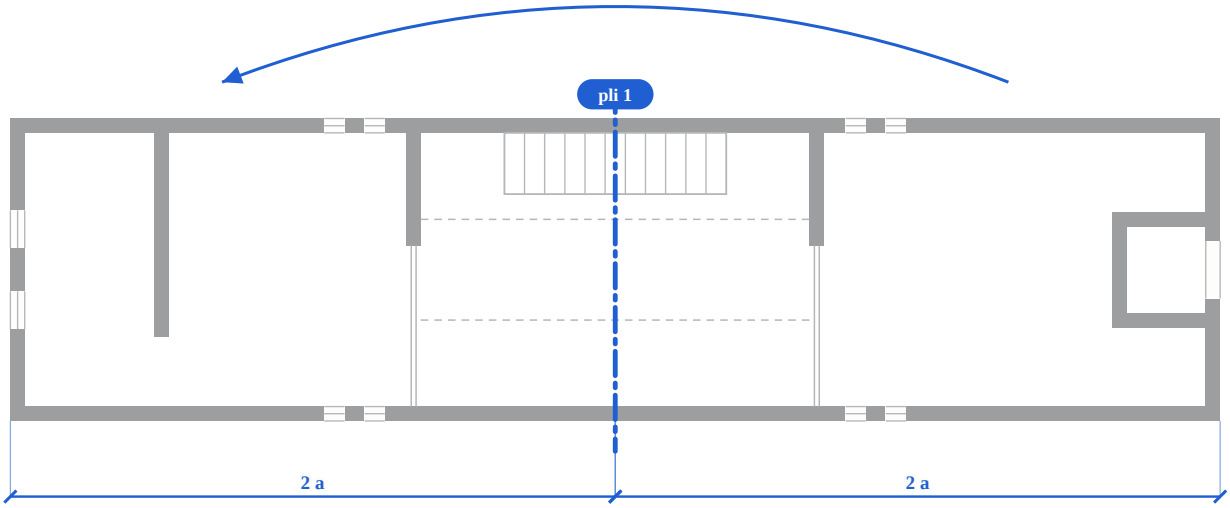

Pli 2 · encore en 2 : 4 carrés a

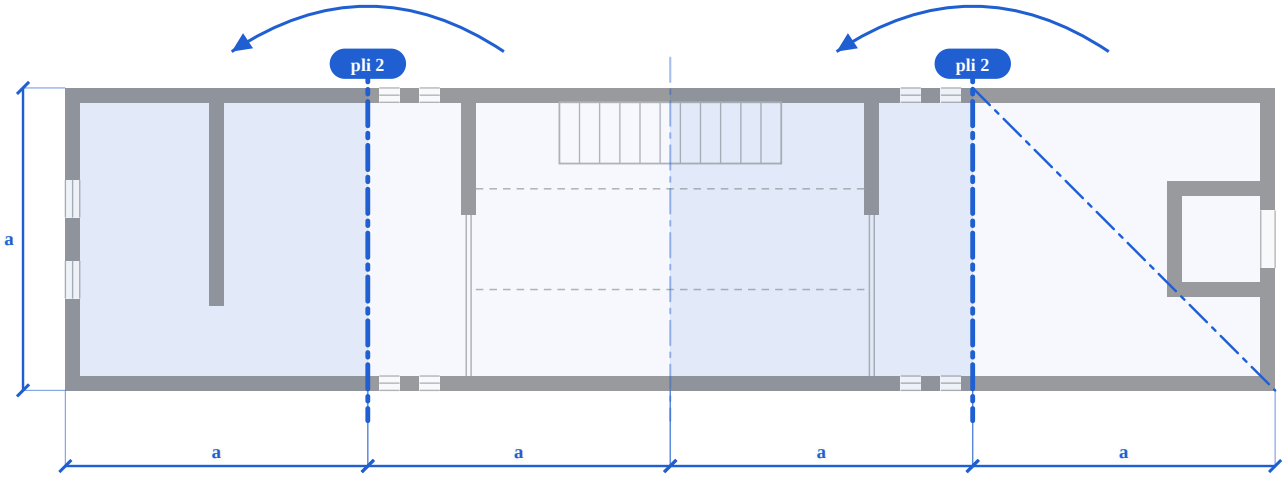

Pli 3 · en 3 : les plis tombent sur les murs du patio

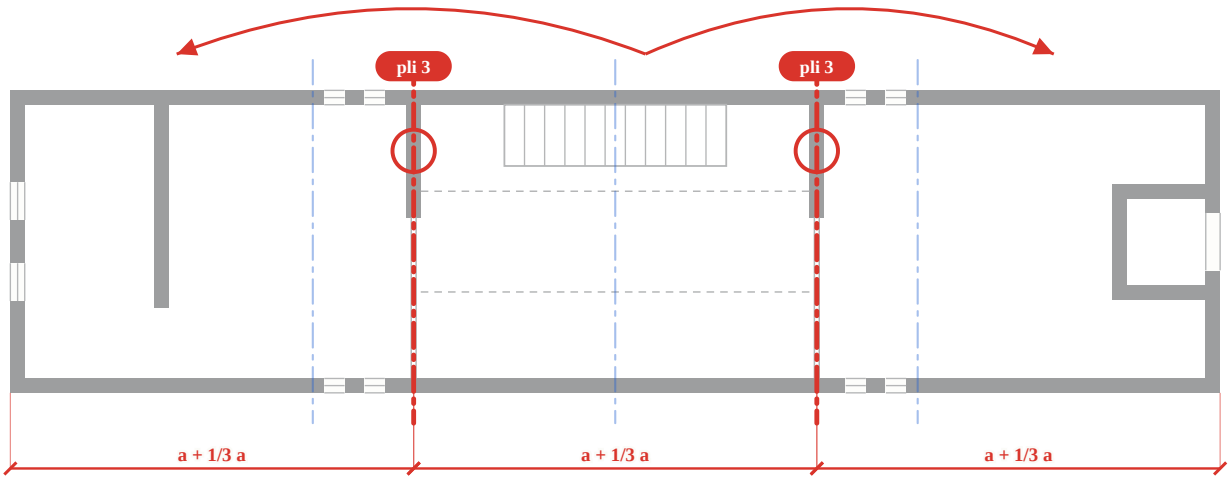


4 cm = a = 4 m

Azuma House · Les plis, étape par étape


Feuille 5 · les plis (2/3) · échelle 1/100 (a = 4 cm) · imprimer à 100 %

plis du carré · plis du tiers · plis du quart · plis du mur

Pli 4 · la largeur en 3 : la trame de 1/3 a

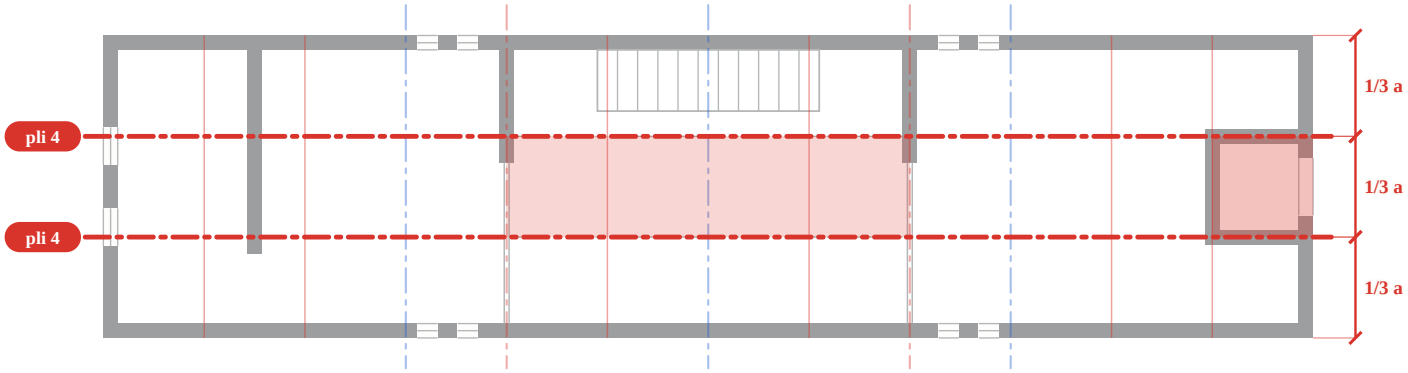

Pli 5 · a en 2, 4, 8 : salle de bain, escalier, porte

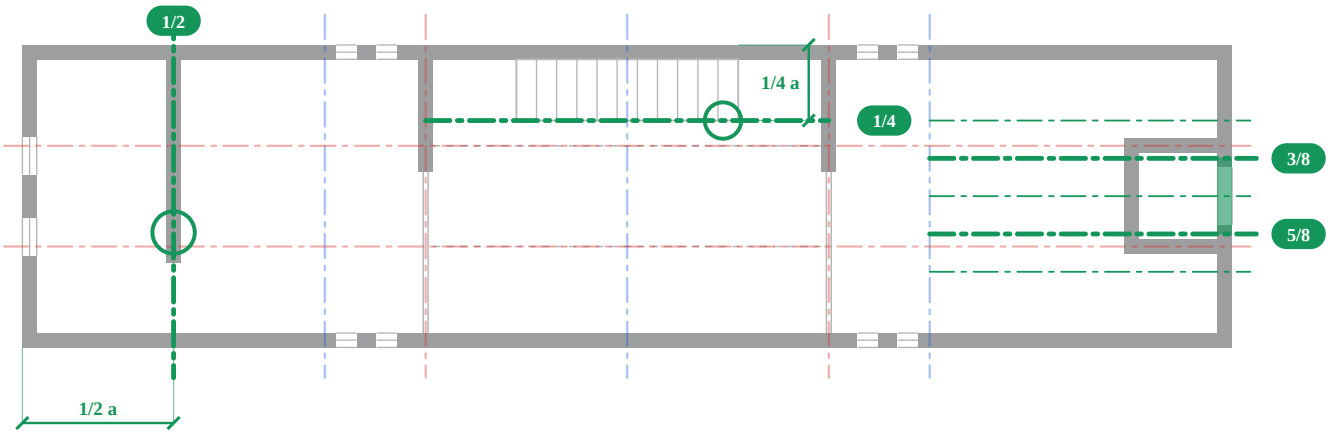


4 cm = a = 4 m

Azuma House · Les plis, étape par étape


Feuille 5 · les plis (3/3) · échelle 1/100 (a = 4 cm) · imprimer à 100 %

plis du carré · plis du tiers · plis du quart · plis du mur

Pli 6 · zoom × 5 : le tiers en 7 = le mur e (au 1/20)

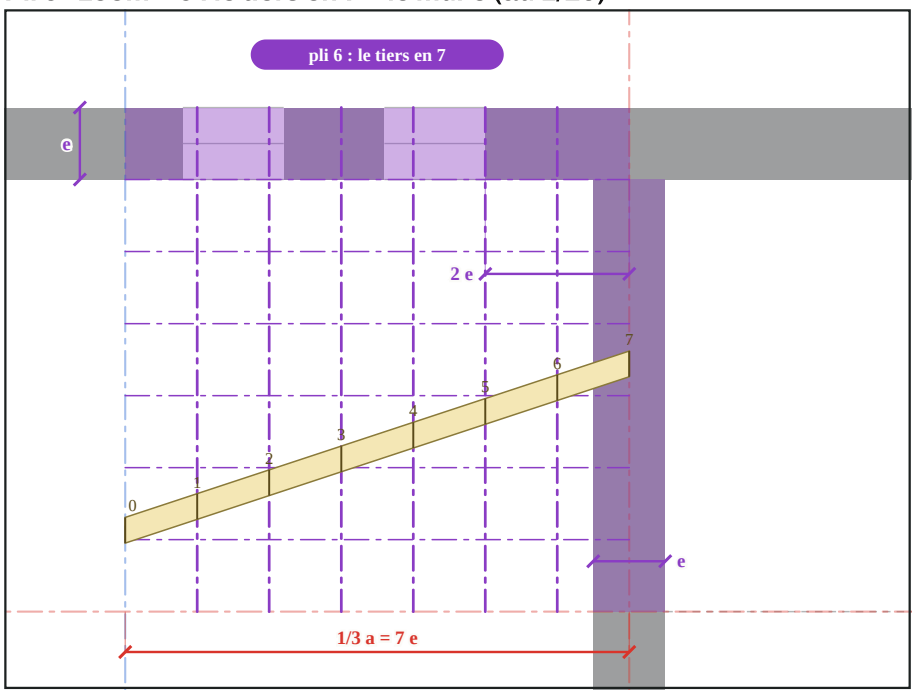

Pli 7 · zoom × 2,5 : le tiers en 5 = 1/15 a, fenêtres et marches (au 1/40)

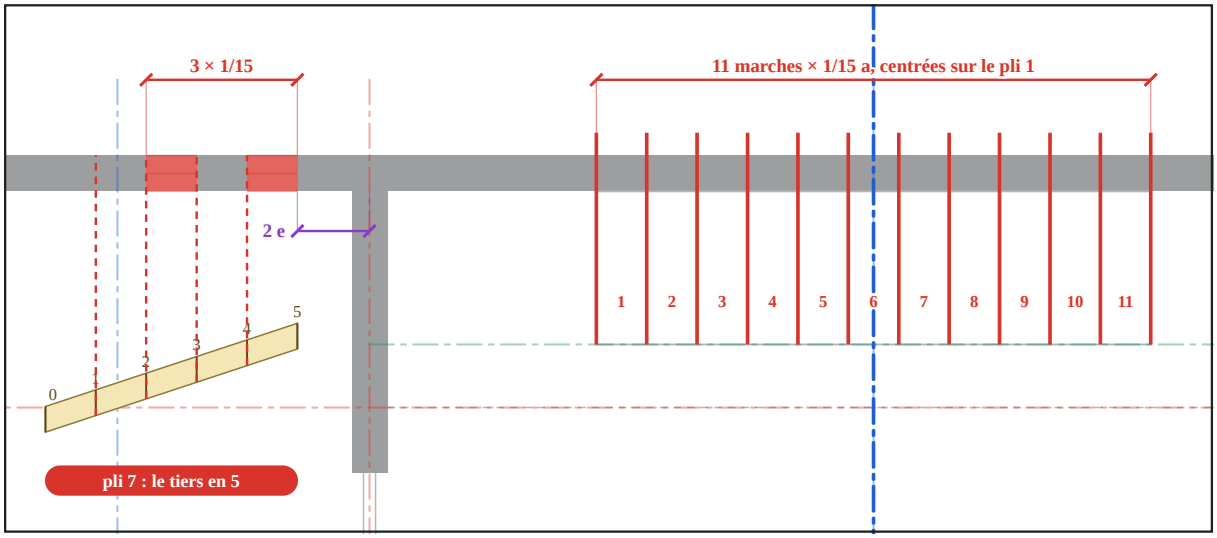

4 cm = a = 4 m