

Azuma House · Base · le bâtiment au trait

Feuille 1 · les plans · échelle 1/100 (a = 4 cm) · imprimer à 100 %


Rez-de-chaussée

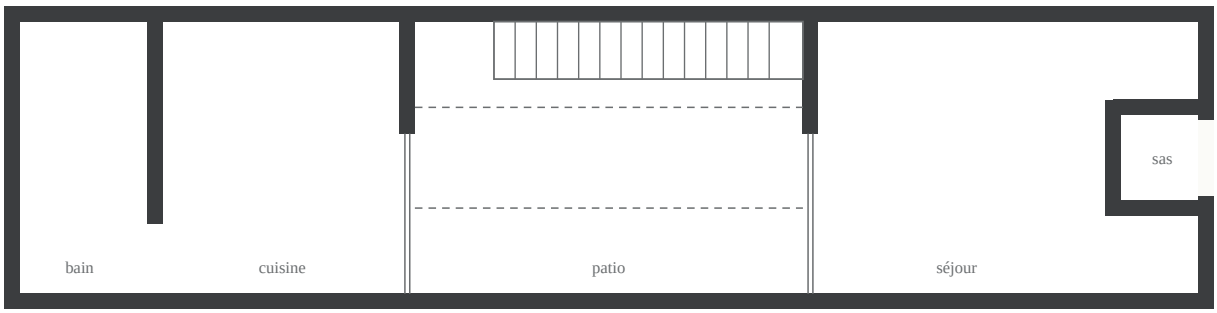

Étage

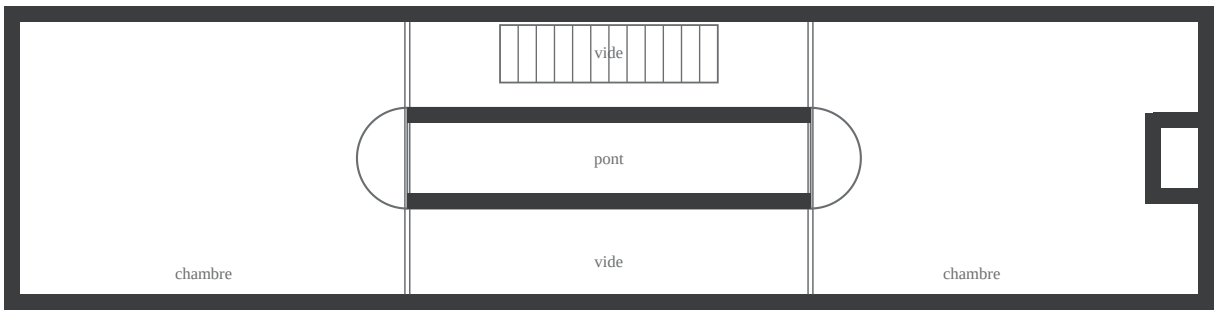

Toiture

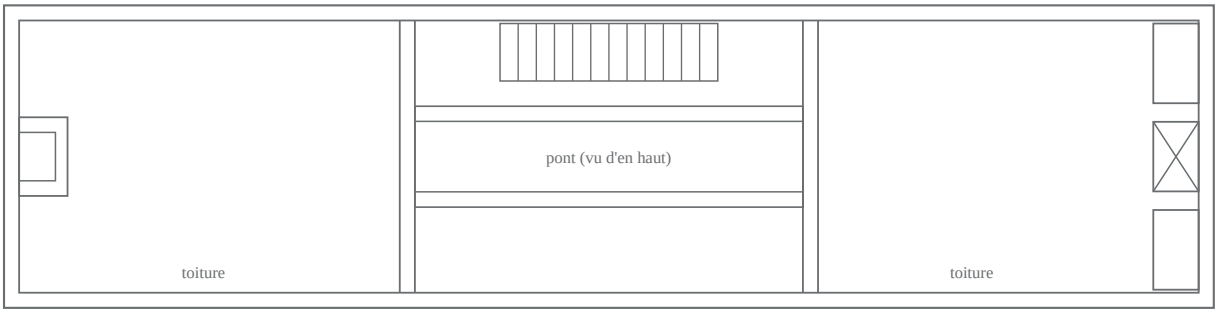


4 cm = a = 4 m

Azuma House · Calque 1 · le carré et le tiers


Feuille 1 · les plans · échelle 1/100 (a = 4 cm) · imprimer à 100 %

a · le carré **1/3 a · le tiers** en gris pâle : repère, à ne pas recopier


Rez-de-chaussée

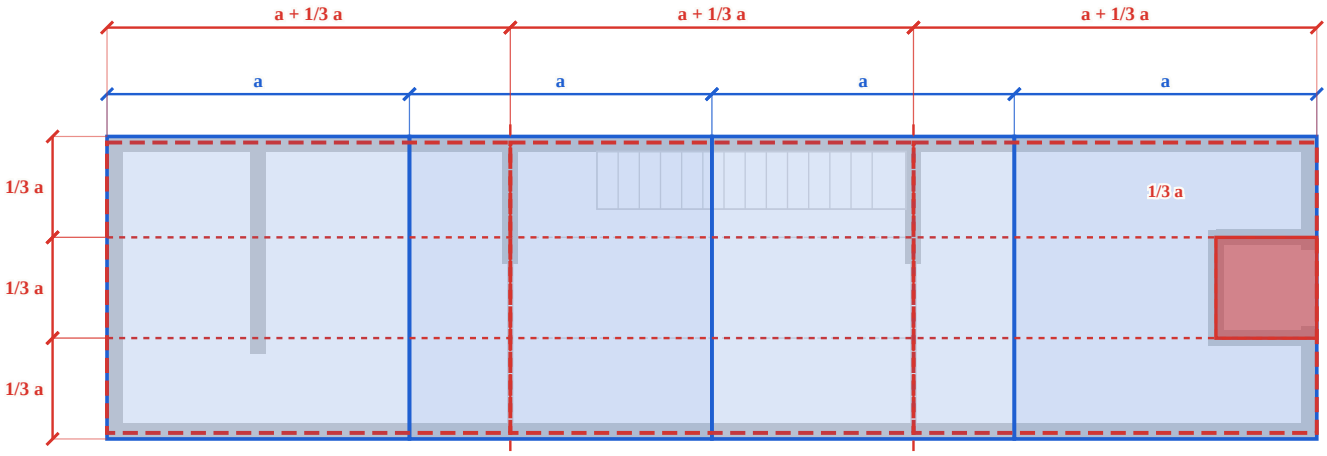

Étage

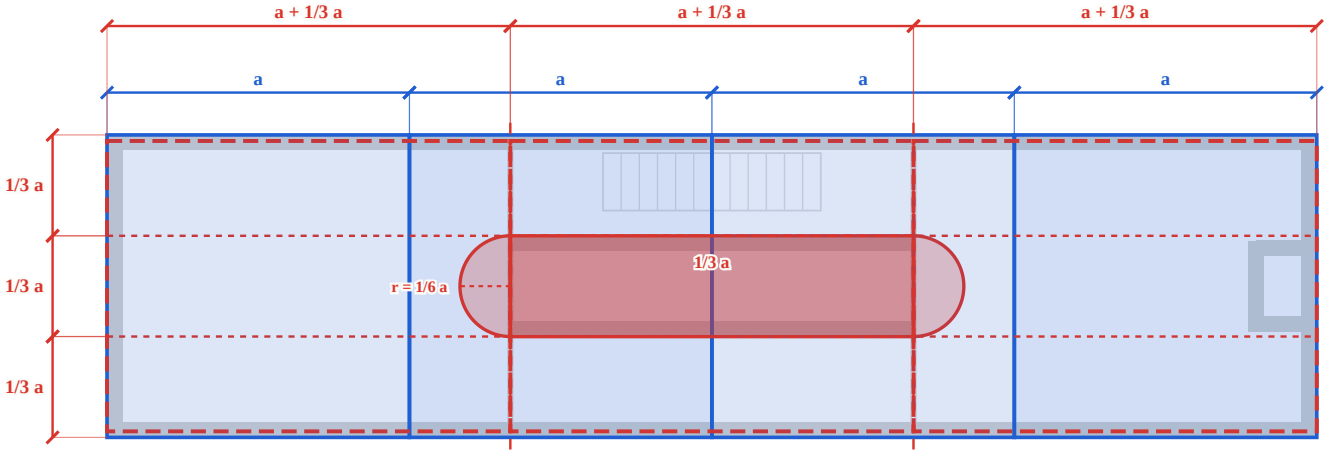

Toiture

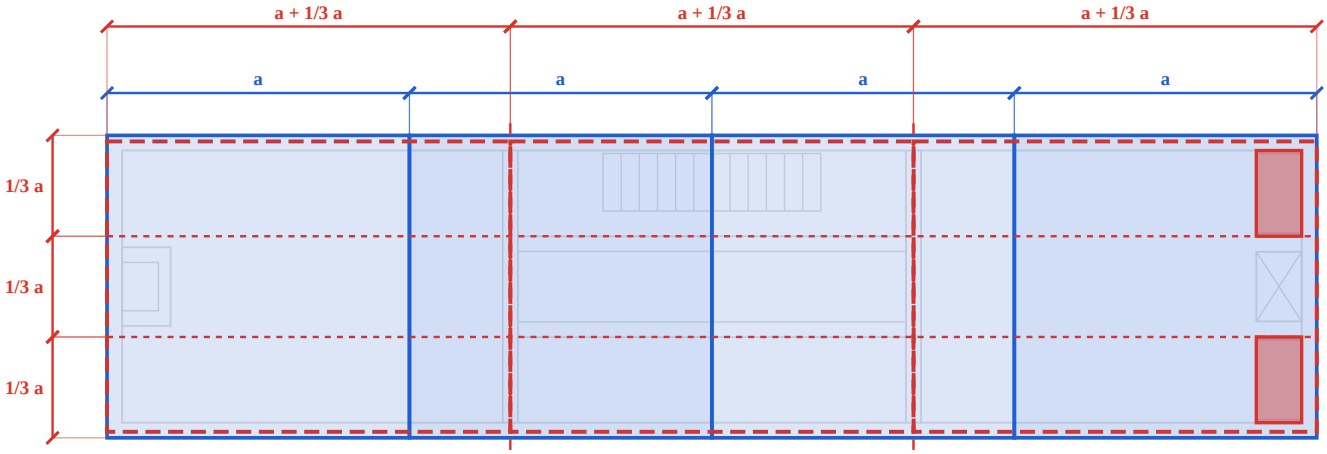


4 cm = a = 4 m

Azuma House · Calque 2 · le quart et le mur


Feuille 1 · les plans · échelle 1/100 (a = 4 cm) · imprimer à 100 %

1/4 a · le quart — **e = 1/20 a · le mur** — en gris pâle : repère, à ne pas recopier


Rez-de-chaussée

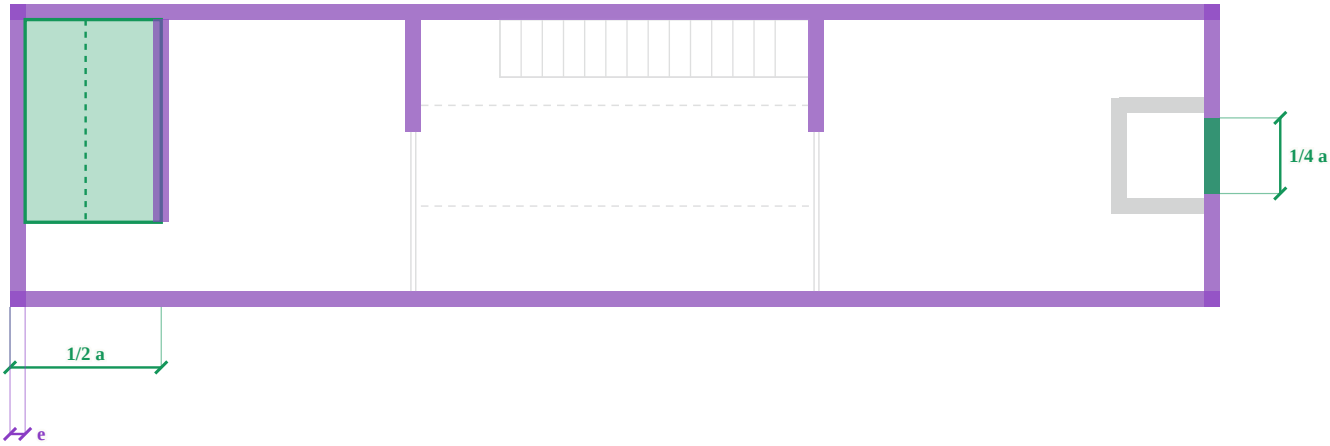

Étage

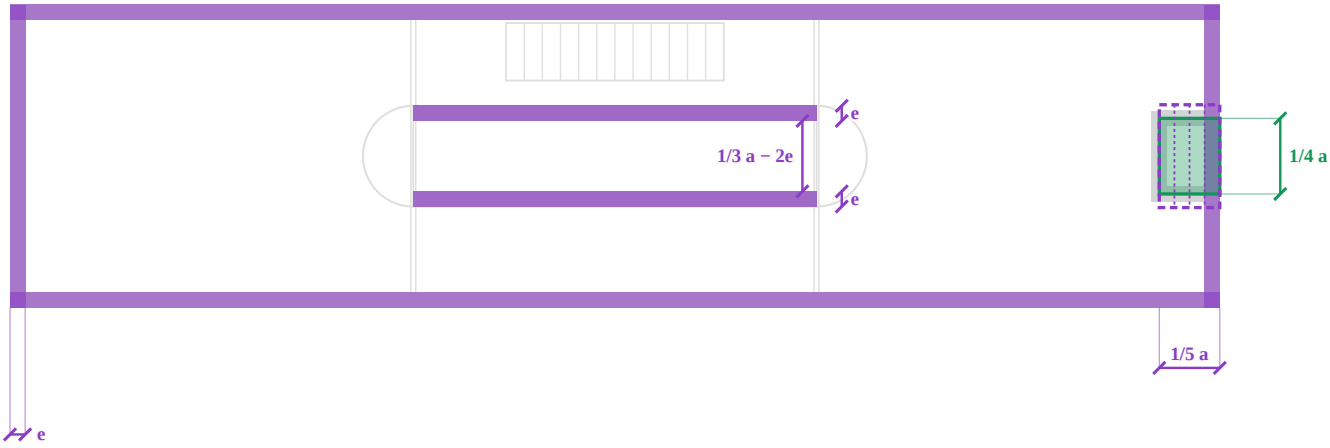

Toiture

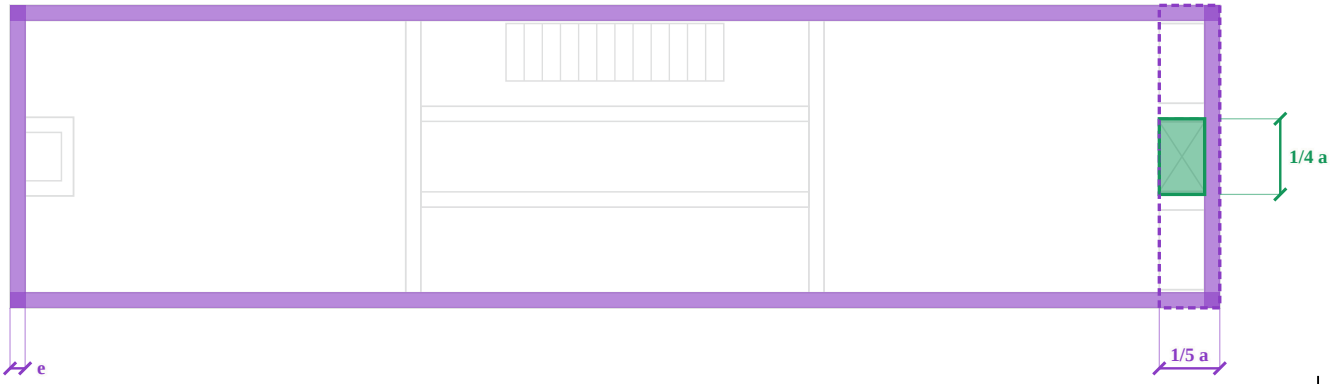


4 cm = a = 4 m


Azuma House · Base · le bâtiment au trait

Feuille 2 · coupe longitudinale, coupe C, façade B · échelle 1/100 (a = 4 cm) · imprimer à 100 %


Coupe longitudinale

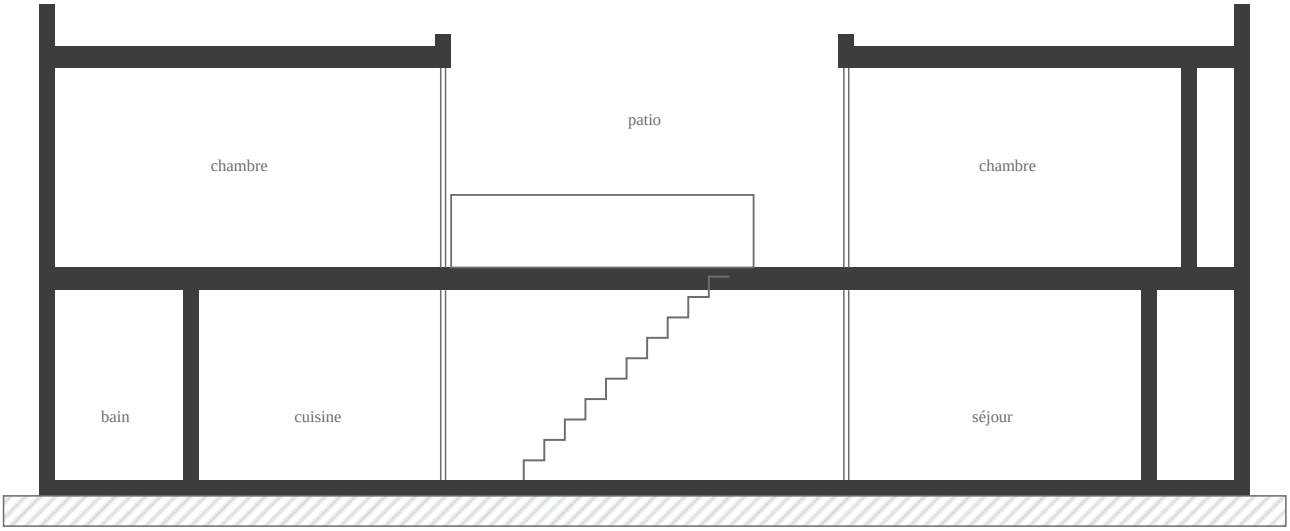

Coupe C

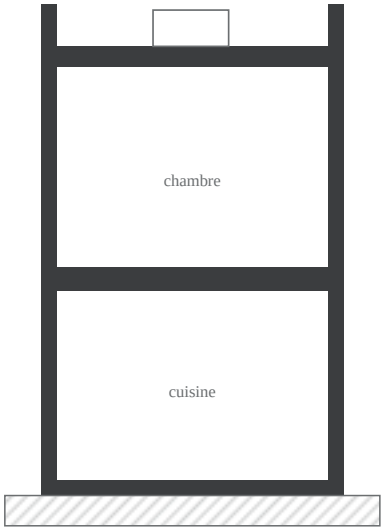

Façade B (rue)

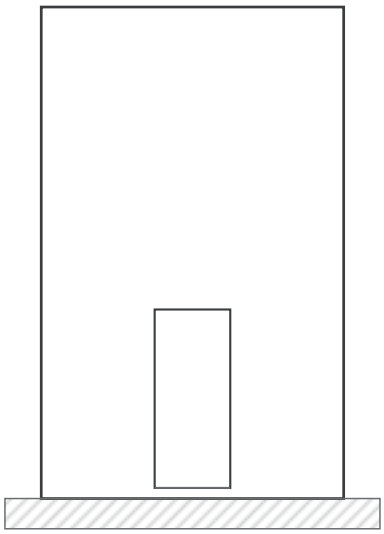


4 cm = a = 4 m

Azuma House · Calque 1 · le carré et le tiers


Feuille 2 · coupe longitudinale, coupe C, façade B · échelle 1/100 (a = 4 cm) · imprimer à 100 %

a · le carré **1/3 a · le tiers** en gris pâle : repère, à ne pas recopier


Coupe longitudinale

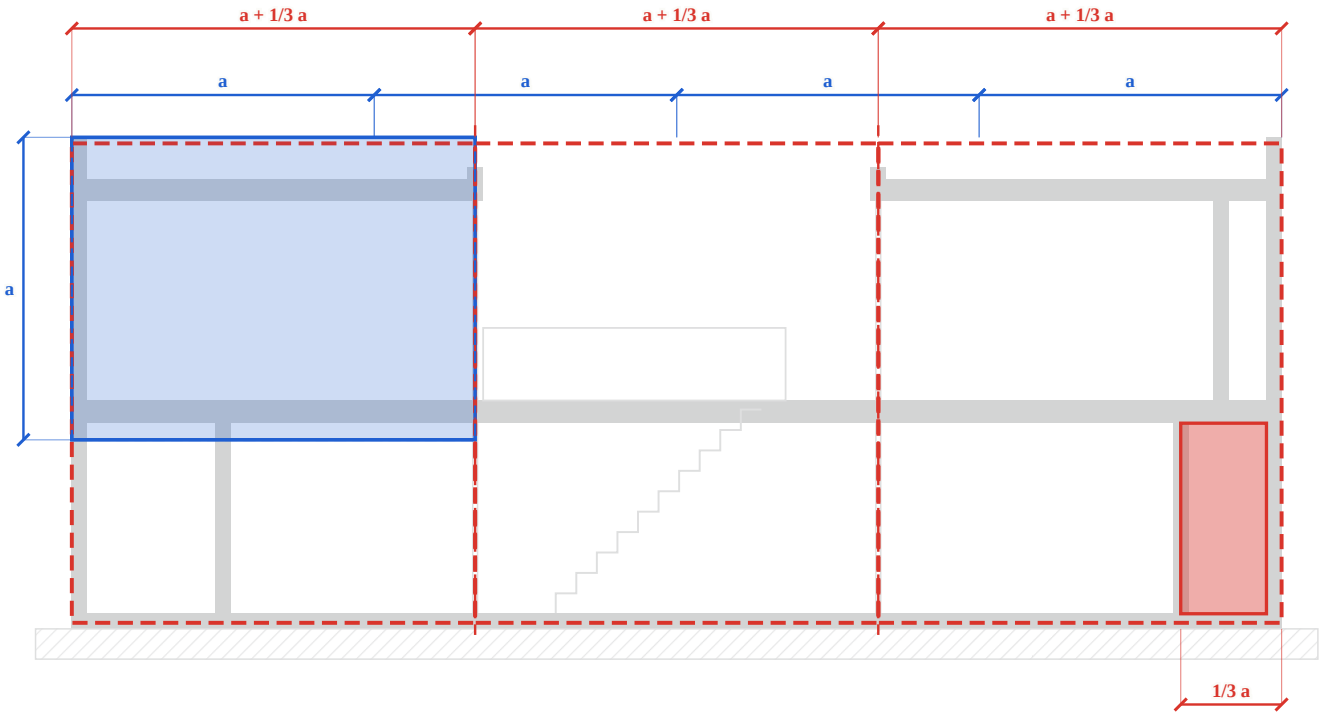

Coupe C

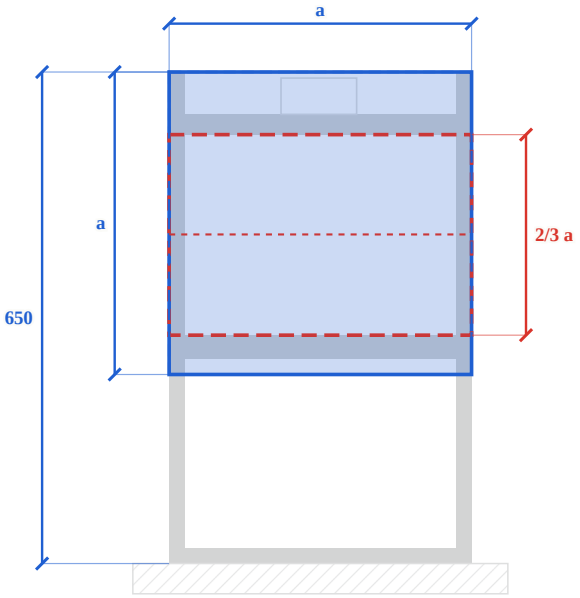

Façade B (rue)

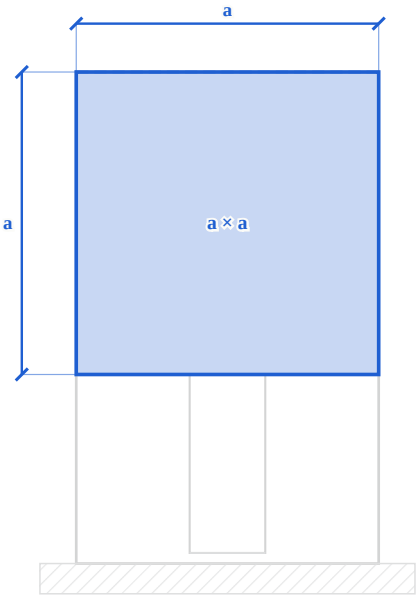


4 cm = a = 4 m

Azuma House · Calque 2 · le quart et le mur


Feuille 2 · coupe longitudinale, coupe C, façade B · échelle 1/100 (a = 4 cm) · imprimer à 100 %

1/4 a · le quart **e = 1/20 a · le mur** en gris pâle : repère, à ne pas recopier


Coupe longitudinale

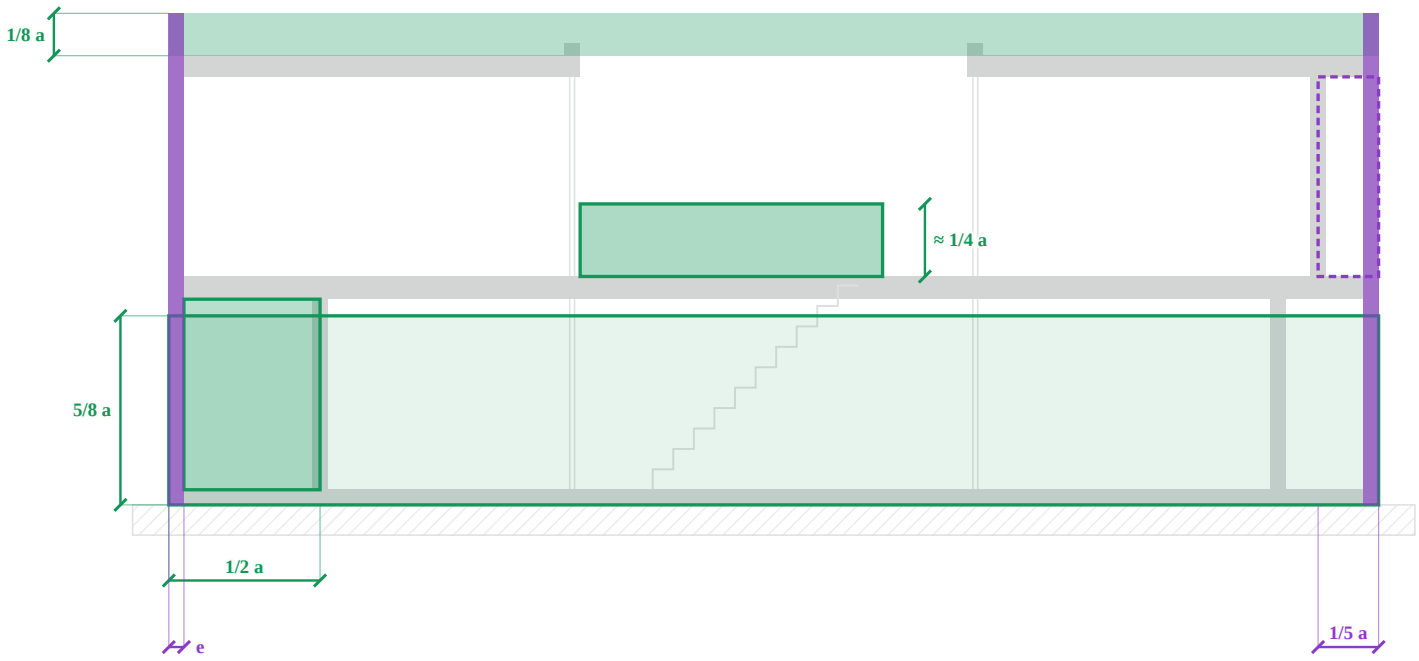

Coupe C

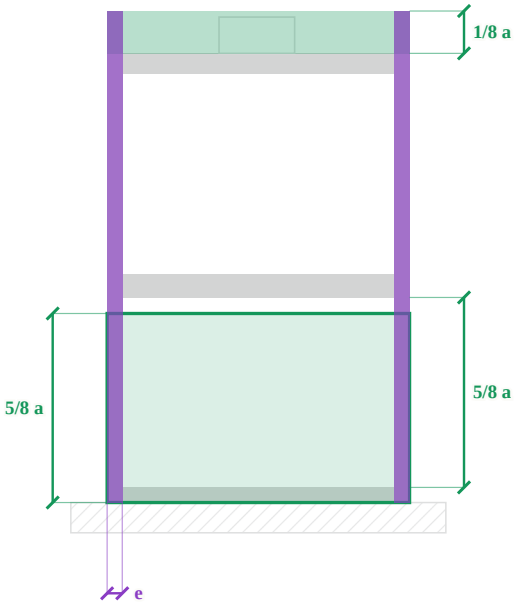

Façade B (rue)

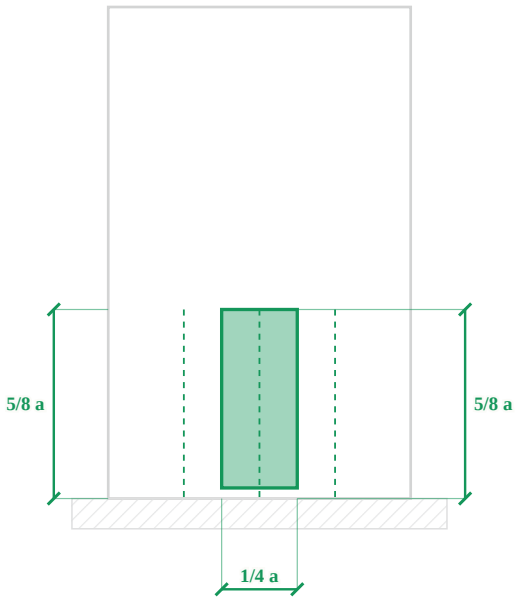


4 cm = a = 4 m


Azuma House · Base · le bâtiment au trait

Feuille 3 · coupe E, façade C · échelle 1/100 (a = 4 cm) · imprimer à 100 %

Coupe E (patio)

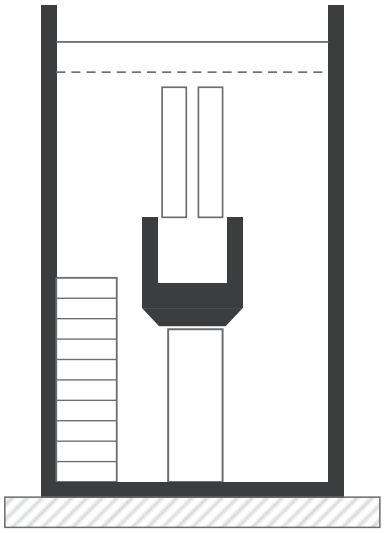

Façade C (jardin)

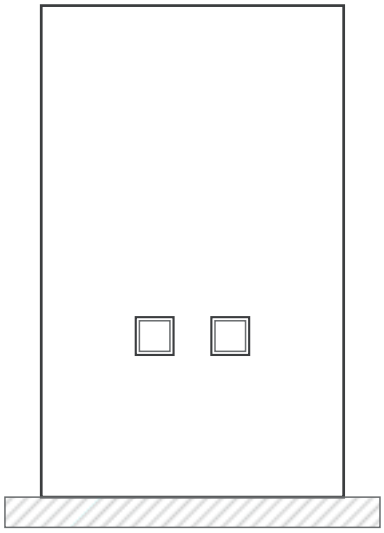


4 cm = a = 4 m

Azuma House · Calque 1 · le carré et le tiers


Feuille 3 · coupe E, façade C · échelle 1/100 (a = 4 cm) · imprimer à 100 %

a · le carré **1/3 a · le tiers** en gris pâle : repère, à ne pas recopier

Coupe E (patio)

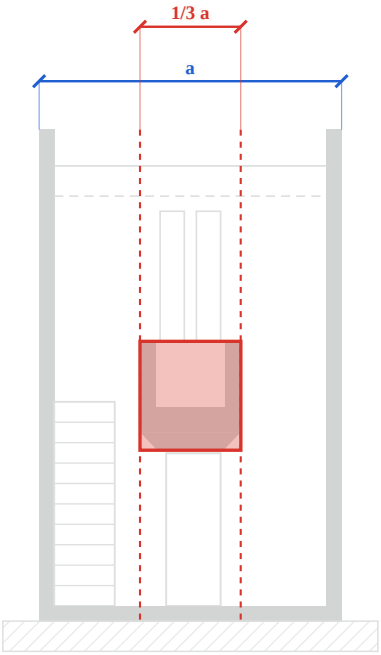

Façade C (jardin)

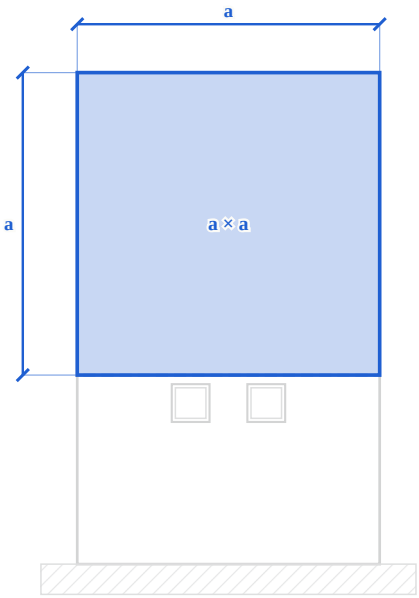


4 cm = a = 4 m

Azuma House · Calque 2 · le quart et le mur


Feuille 3 · coupe E, façade C · échelle 1/100 (a = 4 cm) · imprimer à 100 %

1/4 a · le quart **e = 1/20 a · le mur** en gris pâle : repère, à ne pas recopier

Coupe E (patio)

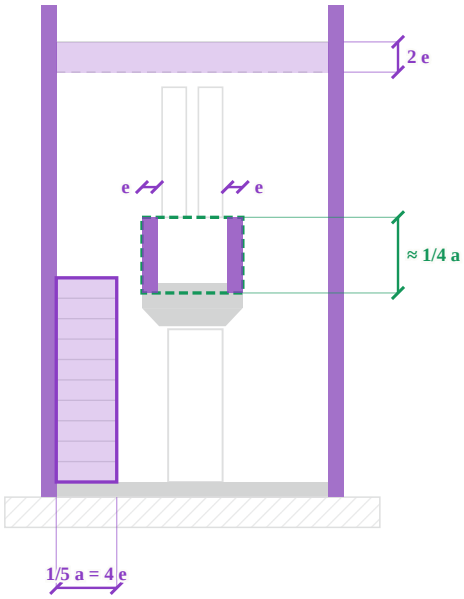

Façade C (jardin)

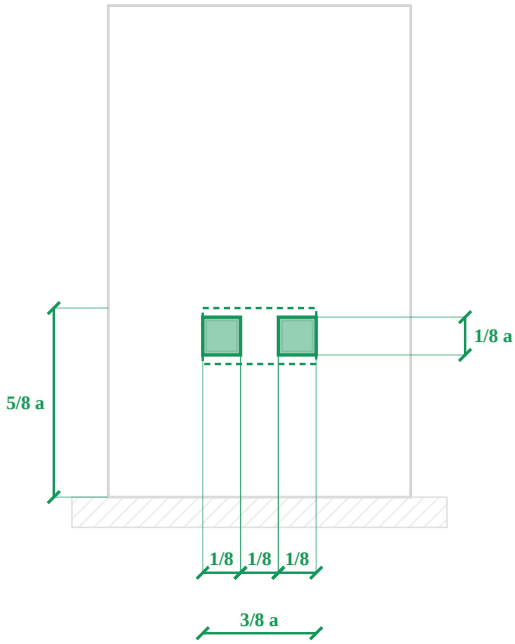

4 cm = a = 4 m